
Kanuni Dönemi (c. 1560) Suriçi İstanbul – Temsili Mimari Çizimler ve Ölçüler

Fatih ilçesi / Tarihî Yarımada · maket kılavuzundaki tüm anıtsal yapılar için plan, kesit ve vaziyet şemaları

İçindekiler

Suriçi Yarımadası – Topoğrafya, Yedi Tepe, Surlar ve İskeleler	2
Yedi Tepe Boy Kesiti ve Rakımlar	3
Kara Surları – Kesit, Kapı ve Burç Planı	4
Su Altyapısı – Bozdoğan Kemeri ve Kırkçeşme Sistemi	5
Eğrikapı Maksemi (Savaklar Çeşmesi) – Plan ve Görünüş	6
Süleymaniye Külliyesi – Vaziyet Planı	7
Süleymaniye Yüksekliği ve Kubbe Çapı Karşılaştırması	8
Şehzade Mehmed Külliyesi	9
Haseki Hürrem Sultan Külliyesi	10
Edirnekapı Mihrimah Sultan Külliyesi	11
Yavuz Sultan Selim Külliyesi	12
Rüstem Paşa Külliyesi (Tahtakale)	13
Fatih Külliyesi (Özgün 1470 Planı)	14
II. Bayezid Külliyesi	15
Ayasofya-i Kebîr (Kanuni Dönemi) ve Haseki Hürrem Çifte Hamamı	16
İbrahim Paşa Sarayı ve Eski Saray (Sarây-ı Atîk)	17
Topkapı Sarayı – Genel Vaziyet Şeması	18
Birinci Avlu ve Bâb-ı Hümâyun	19
İkinci Avlu (Divan Meydanı)	20
Arz Odası (Bâbüssaâde'nin karşısı) – Plan ve Ölçüler	21
Has Oda Kasrı (Hırka-i Saâdet / Mukaddes Emanetler Dairesi)	22
Üçüncü Avlu (Enderun-ı Hümâyun) – Yerleşim Şeması	23
Üçüncü ve Dördüncü Avlu Köşkleri – Plan Şemaları	24
Harem-i Hümâyun – Altı Bölge Şeması	25
Büyük Çarşı (Kapalıçarşı) – Bedestenler ve Çifte Kepenkli Dükkân	26
Elçi Hanı (Divanyolu – Çemberlitaş Karşısı)	27
Hanlar, Saraçhane ve Meslek Bölgeleri – Şemalar	28
16. Yüzyıl İstanbul Evi (Menzil) – Avlu Planı ve Kesit	29
Başoda – İç Mekân Planı ve Duvar Görünüşü	30
Ölçek Stratejisi ve Çeviri Tablosu	31

Okuma kılavuzu

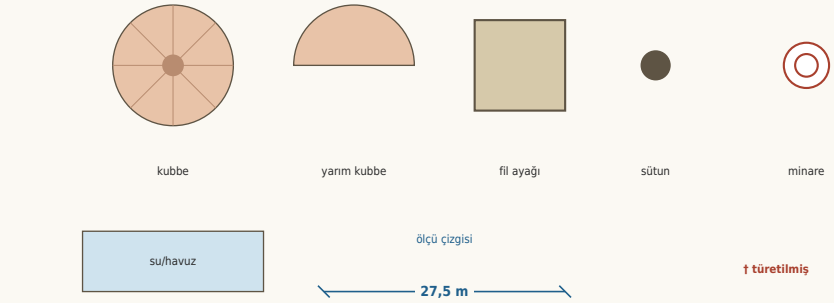

Ölçeksiz / şematik yerleşim

- Her sayfa: sol tarafta çizim, sağ tarafta belgeden alınmış ölçü tablosu ve maket notları.
- "Yaklaşık ölçek" yazan çizimler ölçeklidir (yazdırmada A4 yatay, %100). "Ölçeksiz" olanlar yalnızca düzeni gösterir.
- † işareti: kaynak belgede olmayan, türetilmiş ya da oransal değerdir (örn. eşdeğer kare kenarı, avlu derinliği).
- Yön: aksi belirtilmedikçe kuzey yukarıdır; kıble güneye bakar.
- Temsili şemalardır; ölçülü rölöve veya restitüsyon projesi yerine geçmez. Belgede ölçü verilmeyen yapılarda (Şehzade, Rüstem Paşa, Ayasofya vb.) sayısal düzen (kubbe, ayak, oda adedi) korunmuş, boyutlar oransal bırakılmıştır.


Kronolojik kesit: 1557–1566 (Kanuni'nin son on yılı)

Tamamlanmış: Şehzade (1543–48), Haseki Hürrem (1538–51), Süleymaniye (1550–57), Rüstem Paşa (1555–61), Mihrimah (1562–65), Kırkçeşme Su Sistemi (1554–64).
Makette olmaması gerekenler: Sultanahmet, Yeni Cami/Mısır Çarşısı, Nuruosmaniye, Fatih Camii'nin 1771 yapısı, Kapalıçarşı sokak tonozları, Topkapı'nın 17.–19. yy köşkleri.

Suriçi Yarımadası – Topoğrafya, Yedi Tepe, Surlar ve İskeleler

Genel altlık şeması · 1. bölüm

Maket tabanı: yarımada, tepeler, kapılar, iskele bölgeleri

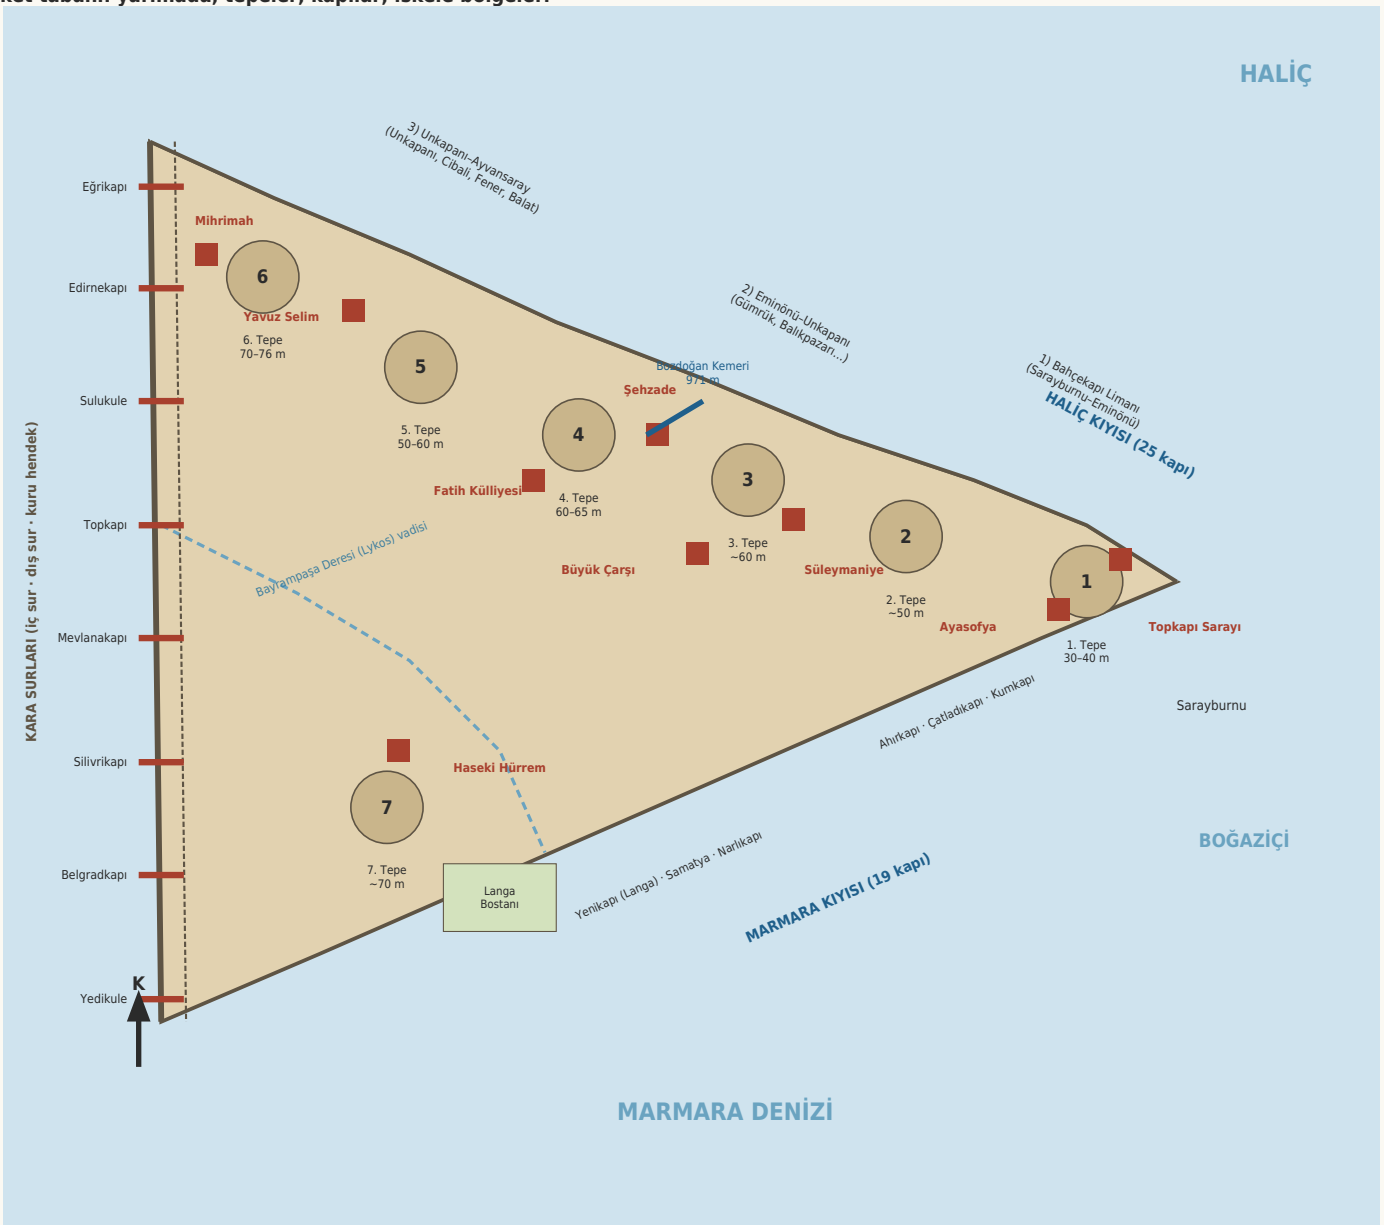

Ölçeksiz / şematik yerleşim

Kapı ve sur sayıları

Toplam sur kapısı	55
Haliç Surları kapısı	25
Marmara Surları kapısı	19
Kara Surları kapısı (türetilmiş)	11 †

Yedi tepe rakımları

1. Tepe (Sarayburnu–Sultanahmet)	30–40 m
2. Tepe (Çemberlitaş)	~50 m
3. Tepe (Beyazıt–Süleymaniye)	~60 m
4. Tepe (Fatih)	60–65 m
5. Tepe (Yavuz Selim)	50–60 m
6. Tepe (Edirnekapı)	70–76 m
7. Tepe (Kocamustafapaşa)	~70 m

Maket notları

Kara surlarındaki hendek 16. yy.da kuru olduğundan toprak renginde yapılmalıdır (Matrakçı, 1537).


Langa (Yenikapı) eski Vlanga Limanı kumla dolup duvarlı bostana dönüşmüştür.

Şema ölçeksizdir; kıyı çizgisi ve tepe konumları yerleşim mantığını göstermek içindir.

Yedi Tepe Boy Kesiti ve Rakımlar

Haliç sırtı (1.–6. tepe) ve Yedinci Tepe · düşey abartılı kesit

Haliç sırtı boy kesiti (doğu → batı) · düşey ölçek yatay ölçeğin ~4 katı

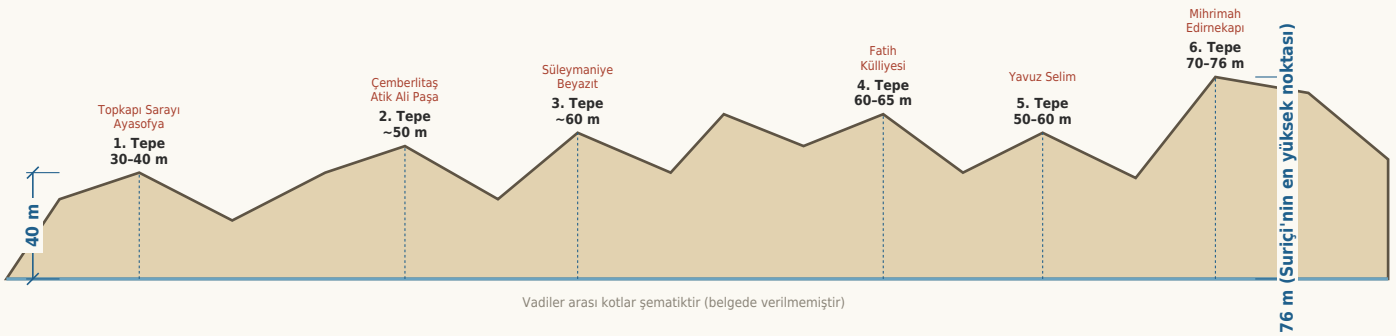

Ölçeksiz / şematik yerleşim

Topoğrafik veriler

Sarayburnu (kıyı–1. tepe)	**0–40 m**
Edirnekapı / 6. Tepe	**76 m**
7. Tepe (Kurutepe)	**~70 m**
Bozdoğan Kemeri azami yükseklik	**28 m**

Maket yapım ipuçları

1:2.000 ölçekte 76 m = 3,8 cm, 40 m = 2,0 cm; yükselti eğrileri katmanlı mukavva/strafor ile verilebilir.


Düşey abartı yapılırsa (örn. 2×) tepelerin göreli sırası korunur; Edirnekapı en yüksek, Sarayburnu en alçak olmalıdır.

7. Tepe, Bayrampaşa Deresi (Lykos) vadisinin güneyinde ayrı bir üçgen plato olarak modellenir; Marmara kıyısına ve kara surlarına hâkimdir.

Kara Surları – Kesit, Kapı ve Burç Planı


Üç kademeli sur sistemi · hendek 16. yy.da kuru

Kara Surları şematik kesit (dış → iç)

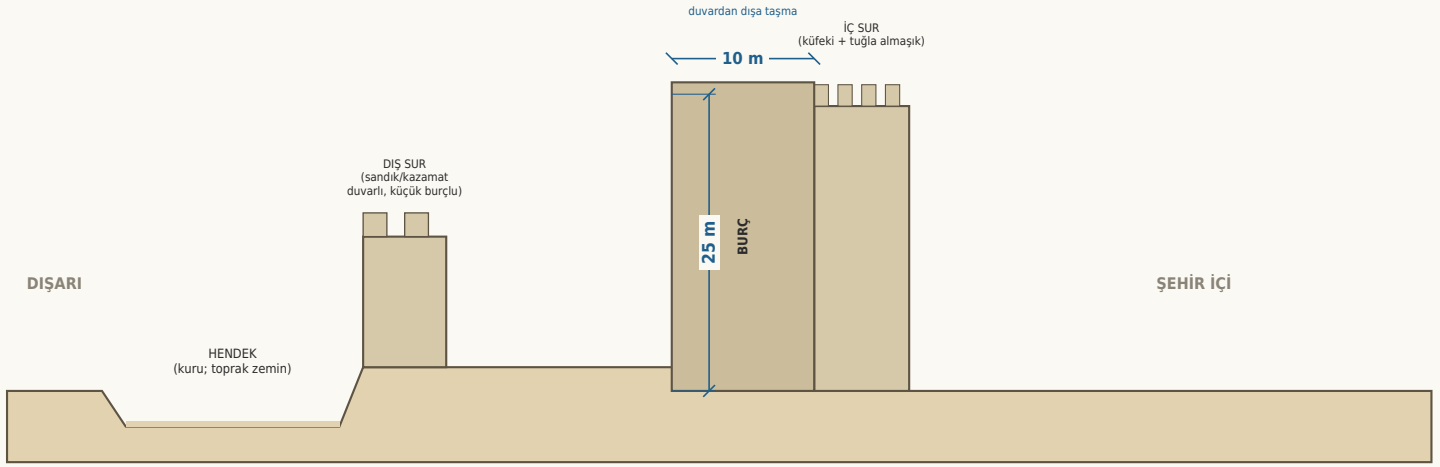


Ölçeksiz / şematik yerleşim

Kapı planı: çifte kule + iç avlu

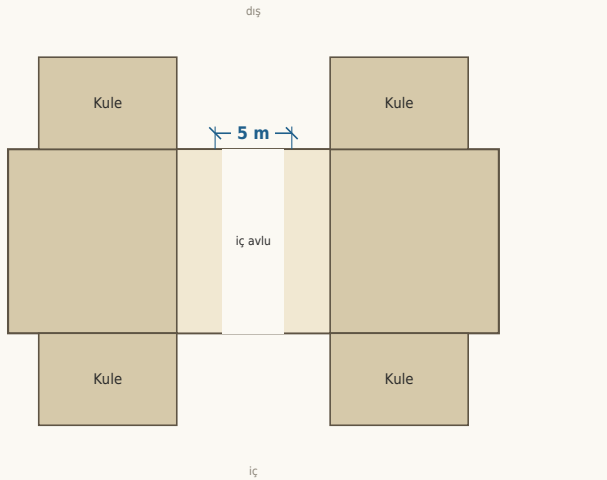

Yaklaşık ölçek 1:490

Burç planı (çoğunlukla kare)

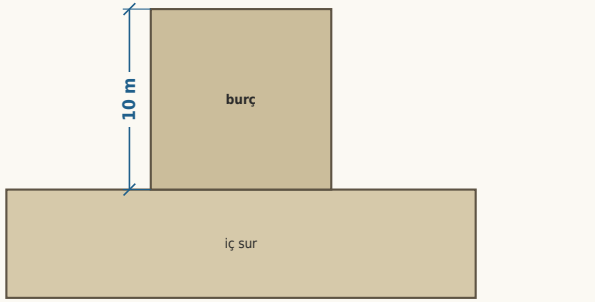

Yaklaşık ölçek 1:420

Sur ölçüleri

Burç yüksekliği	25 m
Burcun surdan taşması	10 m
Sur kapısı kemer genişliği	5 m
Toplam kapı	55
Haliç / Marmara kapı sayısı	25 / 19

Kademeler (içten dışa)

1) İç Sur – küfeki taşı ve tuğla almaşık örgü, yüksek kare burçlu.
2) Dış Sur – sandık/kazamat duvarlı, küçük burçlu.
3) Hendek – 16. yy.da suyu yoktur; zemin toprak rengi.

Ana kara kapıları (kuzey→güney)

Eğrikapı (Kırkçeşme girişi), Edirnekapı (protokol kapısı), Sulukule, Topkapı, Mevlanakapı, Silivrikapı, Belgradkapı, Yedikule.


Yalnız Topkapı ve Edirnekapı iki arabanın yan yana geçebileceği genişliktedir; diğer kapılar dardır.

Kesitteki sur/hendek yükseklik–genişlikleri (25 m ve 10 m dışında) oransaldır †.

Su Altyapısı – Bozdoğan Kemeri ve Kırkçeşme Sistemi


Valens Su Kemeri · Kırkçeşme akış şeması

Bozdoğan (Valens) Su Kemeri – boy görünüşü (tam uzunluk, düşey 10× abartılı)

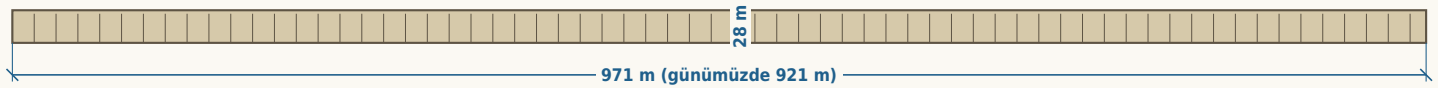


Ölçeksiz / şematik yerleşim

Ayrıntı: iki katlı kemer dizisi (en yüksek yerde 28 m)

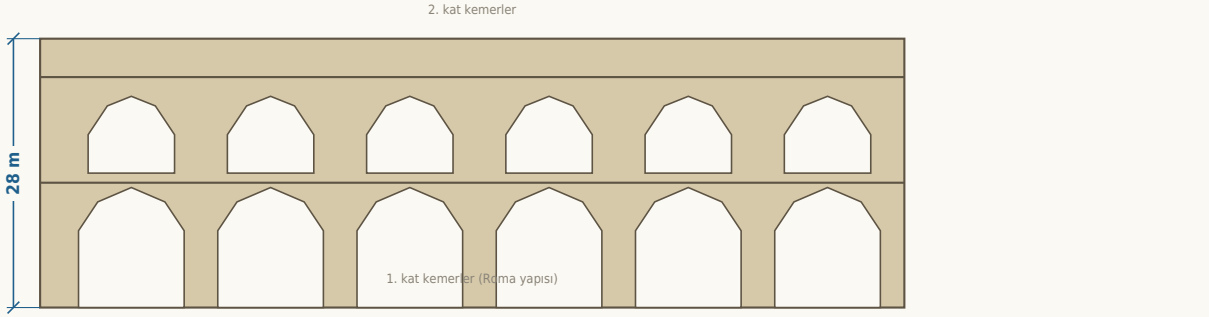

Yaklaşık ölçek 1:790

Kırkçeşme Su Sistemi – akış şeması (ölçeksiz)

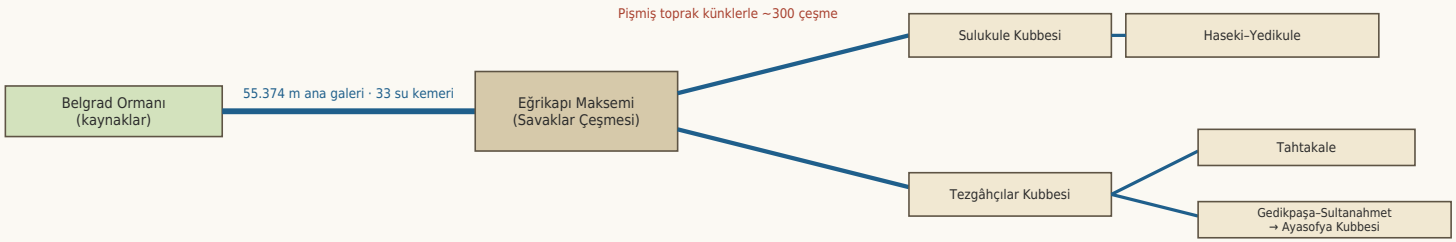

Ölçeksiz / şematik yerleşim

Bozdoğan (Valens) Kemeri

Uzunluk	**971 m (bugün 921 m)**
En yüksek yer	**28 m**
Kat sayısı	**2 (Roma yapısı)**

4. Tepe (Fatih) ile 3. Tepe arasındaki vadiyi aşar; Eski Saray, Süleymaniye, Beyazıt ve Topkapı Sarayı'na su taşır. Yakınında kare planlı kesme taş su terazileri yer alır.

Kırkçeşme Su Sistemi


Yapım	**1554–1563/64**
Maliyet	**50 milyon akçe**
Ana galeri	**55.374 m**
Su kemeri	**33 adet**
Suriçi'ne giriş	**Eğrikapı Maksemi**
Çeşme sayısı (Sinan dönemi)	**~300**

20 Eylül 1563 selinde hasar görmüş, 1564'te onarılmıştır.

Eğrikapı Maksemi (Savaklar Çeşmesi) – Plan ve Görünüş

Kırkçeşme suyunun Suriçi'ne giriş yapısı

Kat planı

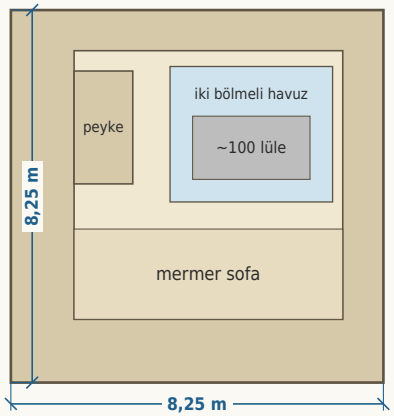


iç mekân 5,95 × 5,95 m

Yaklaşık ölçek 1:170

0 5 m

Görünüş / kesit (şematik)

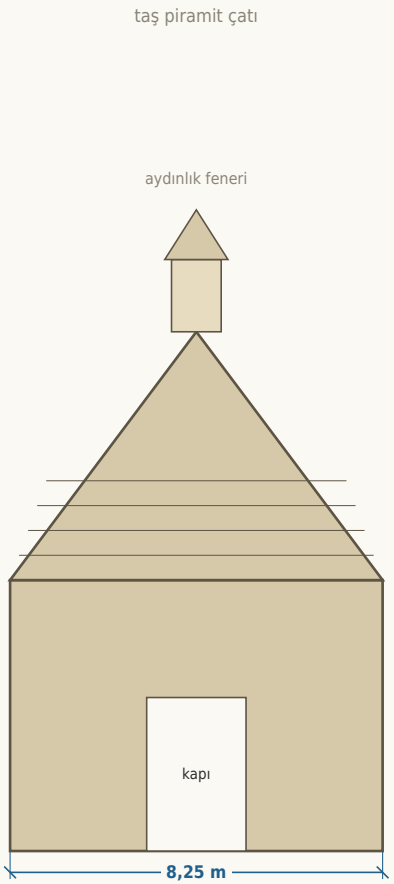

Yaklaşık ölçek 1:170

0 5 m

Ölçüler

Dış plan	**8,25 × 8,25 m**
İç mekân	**5,95 × 5,95 m**
Örtü	**Taş piramit + fener**
Tunç lüle sayısı	**~100**

İç donatı

Mermer döşeli sofa; sağda iki basamaklı taş peyke; ortada mermer set üzerinde iki bölmeli havuz ve suyu ölçerek bölen tunç lüleler.


Maket notu

Yapı Eğrikapı surunun hemen dışındadır. Bugünkü üst örtü II. Mahmud devri onarımını yansıtır; temellerinde Bizans izleri vardır, yükseklikler oransaldır †.

Süleymaniye Külliyesi – Vaziyet Planı

3. Tepe · 1550–1557 · Mimar Sinan · ~60.000 m²

Külliye vaziyet planı (kuzey yukarı, kıble aşağı)

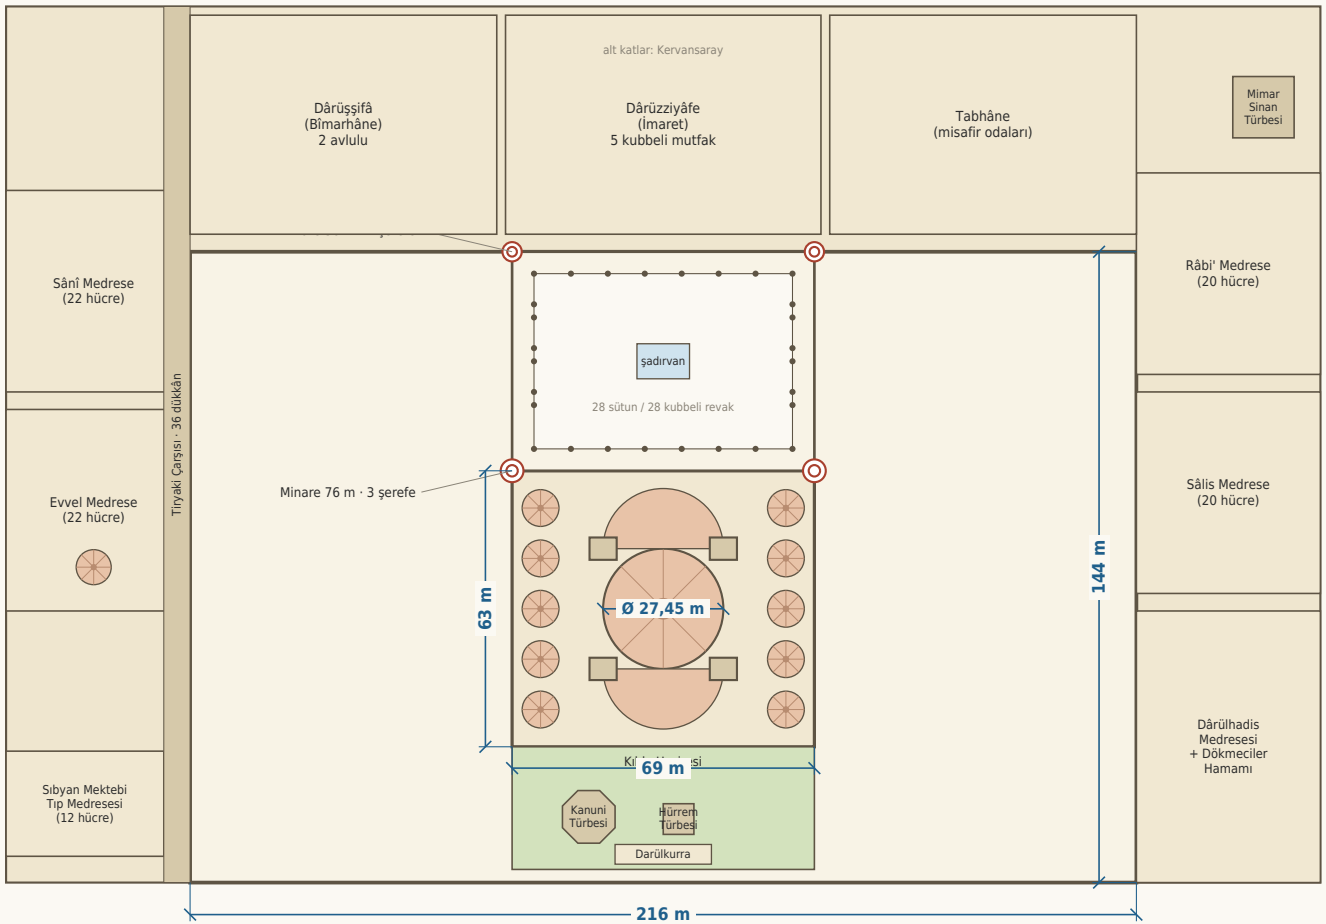

Yaklaşık ölçek 1:1.700

Ana ölçüler

Külliye alanı	**~60.000 m²**
Dış avlu	**216 × 144 m**
Cami harimi	**69 × 63 m**
Ana kubbe çapı	**27,40–27,50 m**
Ana kubbe yüksekliği	**49,50–53 m**
Fil ayağı	**6,20 × 5,10 m**
Kasnak penceresi	**32**
Revak	**28 sütun / 28 kubbe**
Harime bitişik minareler	**76 m · 3 şerefe**
Avlu minareleri	**56 m · 2 şerefe**
Toplam şerefe	**10 (4 minare)**

Kanatlar


Batı: Sıbyan, Tıp, Evvel–Sânî Medreseleri, 36 dükkânlı Tiryaki Çarşısı. Kuzey: Dârüşşifâ, İmaret, Tabhâne (altta Kervansaray). Doğu: Sâlis–Râbi' Medreseleri, Dârülhadis, Dökmeciler Hamamı, Mimar Sinan Türbesi. Güney: hazire.

Avlu derinliği (50 m) ve kanat blokları oransaldır †; toplam saha 300 × 200 m eşdeğeri olarak alınmıştır †.

Süleymaniye Yüksekliği ve Kubbe Çapı Karşılaştırması


Doğu görünüşü ve külliyelerin ana kubbeleri aynı ölçekte

Süleymaniye Camii – doğu görünüşü (şematik)

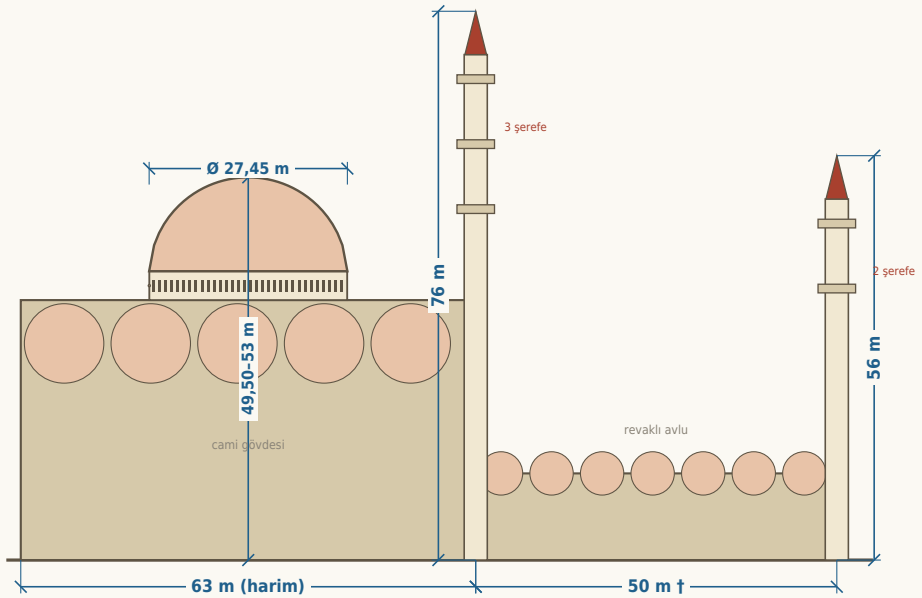

Yaklaşık ölçek 1:1.000

Ana kubbe karşılaştırması (aynı ölçek) – plan çapı ve silüet

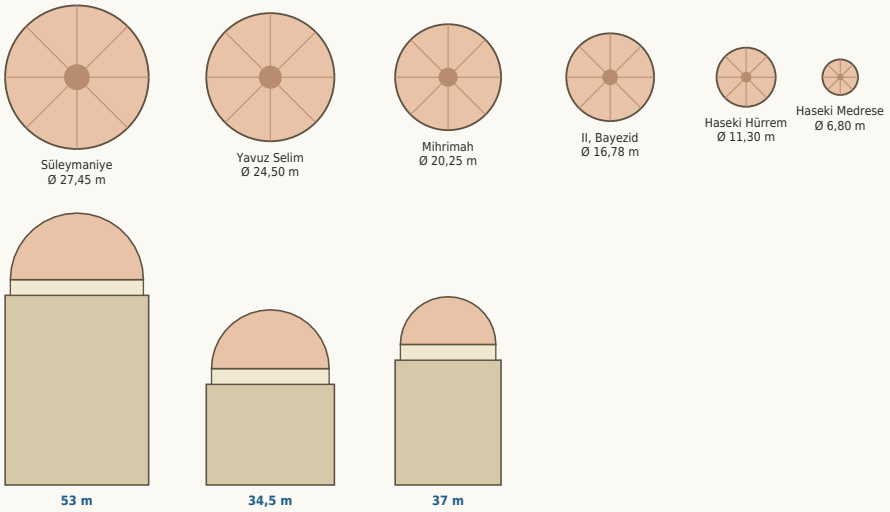

Yaklaşık ölçek 1:1.400

Silüet: kubbe altı gövde yükseklikleri oransaldır †; yalnız toplam yükseklik belgeden alınmıştır

Süleymaniye yükseklikleri

Ana kubbe yüksekliği	**49,50–53 m**
Ana kubbe çapı	**27,40–27,50 m**
Harime bitişik minare	**76 m**
Avlu minaresi	**56 m**

Diğer kubbeler

Yavuz Selim: çap / yükseklik	**~24,5 / 34,5 m**
Mihrimah: çap / yükseklik	**20,25 / 37 m**
II. Bayezid ana kubbe çapı	**16,78 m**
Haseki Hürrem cami kubbesi	**11,30 m**
Haseki Medrese dershane kubbesi	**6,80 m**


1:2.000 ölçekte Süleymaniye kubbesi 1,37 cm, 76 m'lik minare 3,8 cm olur. 1:500 ölçekte kubbe 5,5 cm, 76 m minare 15,2 cm olur †.

Temsili şema. Boyutlar belgedeki verilerden alınmıştır; † işaretli değerler türetilmiş / oransal / kaynakta bulunmayan varsayımdır. Ölçek A4 yatay %100 yazdırmada geçerlidir.

Şehzade Mehmed Külliyesi

3.–4. Tepe arası · 1543–1548 · Mimar Sinan · modüler plan

Vaziyet şeması: harim ve avlu eşit iki kare modül (1 modül = harim kenarı)

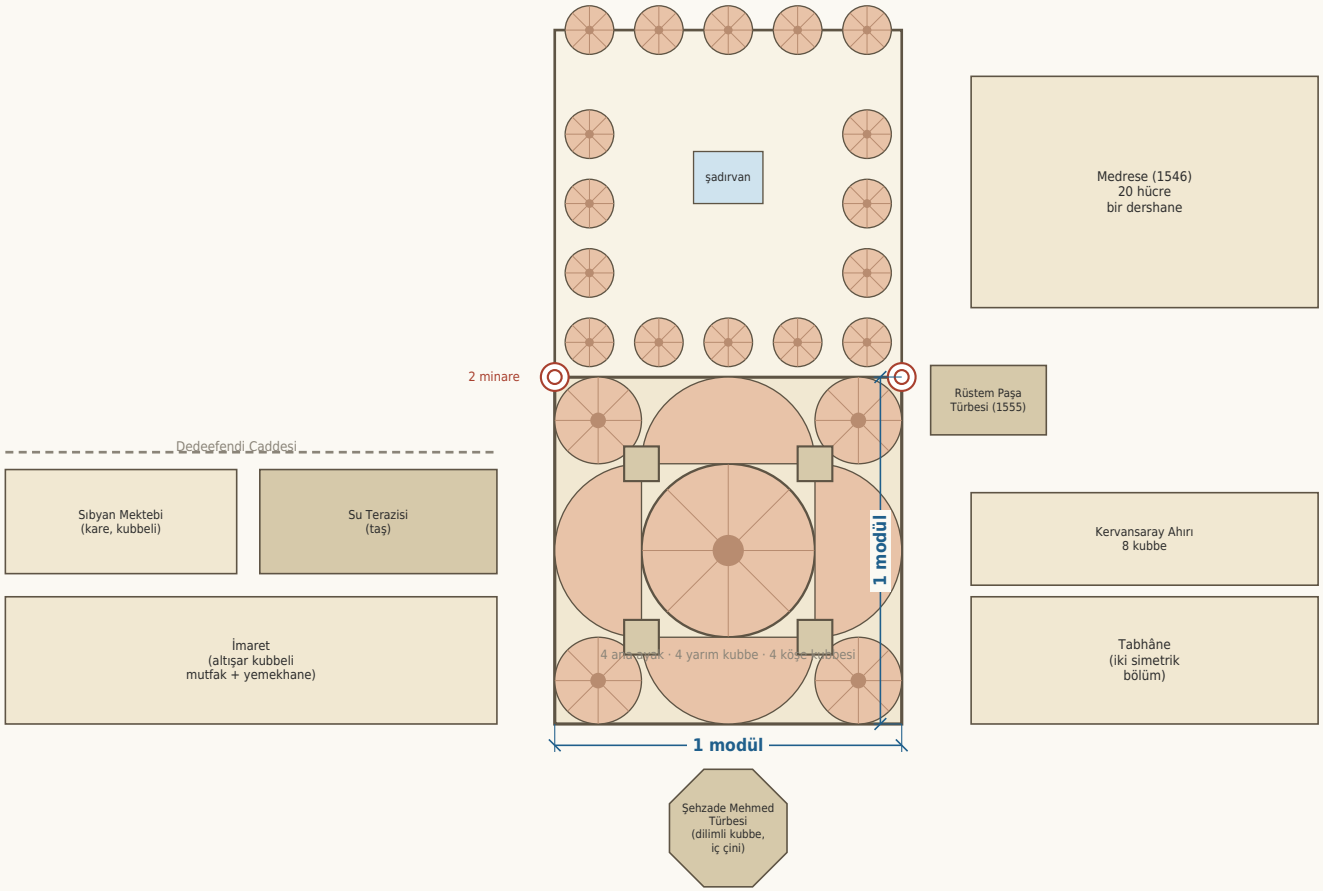

Ölçeksiz / şematik yerleşim

Plan kuralı

Harim ve avlu iki eşit kare modüldür. Merkezî kubbe 4 büyük ayak üzerinde 4 yarım kubbe ve 4 köşe kubbesi ile desteklenir; payandalar yan revaklı galeriler içine gizlenmiştir. İki minareli.

Alt birimler

Medrese (1546)	**20 hücre**
Tabhâne	**2 simetrik**
Kervansaray Ahırı	**8 kubbe**


Hazirede dilimli kubbeli, içi tamamen çini kaplı Şehzade Mehmed Türbesi ve Rüstem Paşa Türbesi (1555) bulunur; diğer dört türbe 1586–1694 ekidir, maketlenmemelidir.

Belgede metrik ölçü verilmediğinden çizim oransaldır †.

Haseki Hürrem Sultan Külliyesi

7. Tepe (Avratpazarı) · 1538–1551 · Mimar Sinan

Vaziyet planı (kuzey yukarı); cami ve medrese kubbe çapları gerçek ölçekli

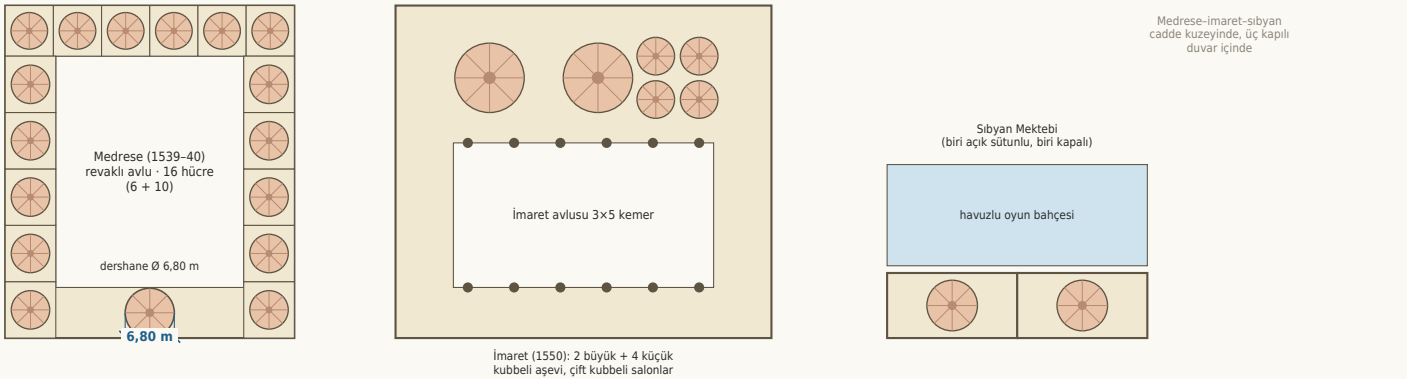

Yaklaşık ölçek 1:1.000

Ölçüler

Cami harimi (kare)	**~11,3 m †**
Cami kubbesi çapı	**11,30 m**
Minare	**1**
Son cemaat yeri	**5 kubbe**
Medrese dershane kubbesi	**6,80 m**
Medrese odaları	**6 + 10 = 16**
İmaret avlusu	**3 × 5 kemer**
Aşevi kubbeleri	**2 büyük + 4 küçük**

Maket uyarısı


1612'de Sedefkâr Mehmed Ağa'nın eklediği ikinci kubbe Kanuni devrinde yoktur. Cami caddenin güneyinde, medrese–imaret–sıbyan–dârüşşifâ kuzey/güney karşılıklı konumlanır.

Birim mesafeleri ve avlu boyutları oransaldır †.

Edirnekapı Mihrimah Sultan Külliyesi

6. Tepe · 1562–1565 · Mimar Sinan

Vaziyet planı (kuzey yukarı)

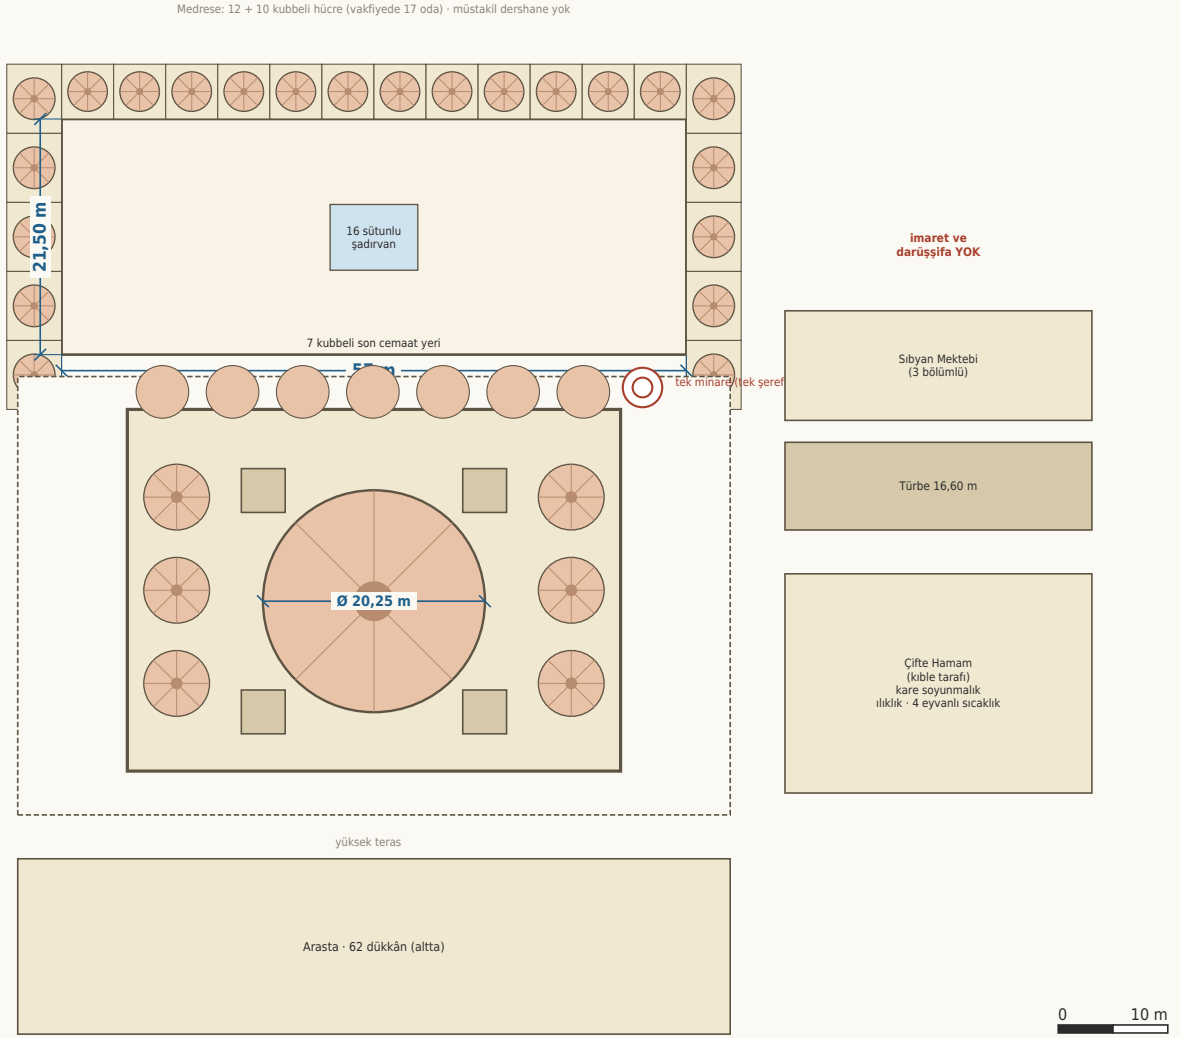

Yaklaşık ölçek 1:690

Ölçüler

Ana kubbe çapı	**20,25 m**
Ana kubbe yüksekliği	**37 m**
Dış avlu	**57 × 21,50 m**
Şadırvan	**16 sütunlu**
Medrese hücreleri	**12 + 10 (vakfiye: 17)**
Arasta	**62 dükkân**
Türbe uzunluğu	**16,60 m**
Son cemaat yeri	**7 kubbe**
Minare	**1 (tek şerefe)**


Mimari

Yüksek teras üzerinde dikdörtgen harim; 4 büyük kemer ve köşe ağırlık kuleleriyle desteklenen çok pencereli ana kubbe; yanlarda ikişer sütunla ayrılan üçer kubbeli alçak yan kanatlar. Hünkâr mahfili yoktur; imaret ve darüşşifası yoktur.

Harim boyutları ve yerleşim mesafeleri oransaldır †.

Yavuz Sultan Selim Külliyesi

5. Tepe (Çarşamba) · 1522 (Kanuni tamamlattı)

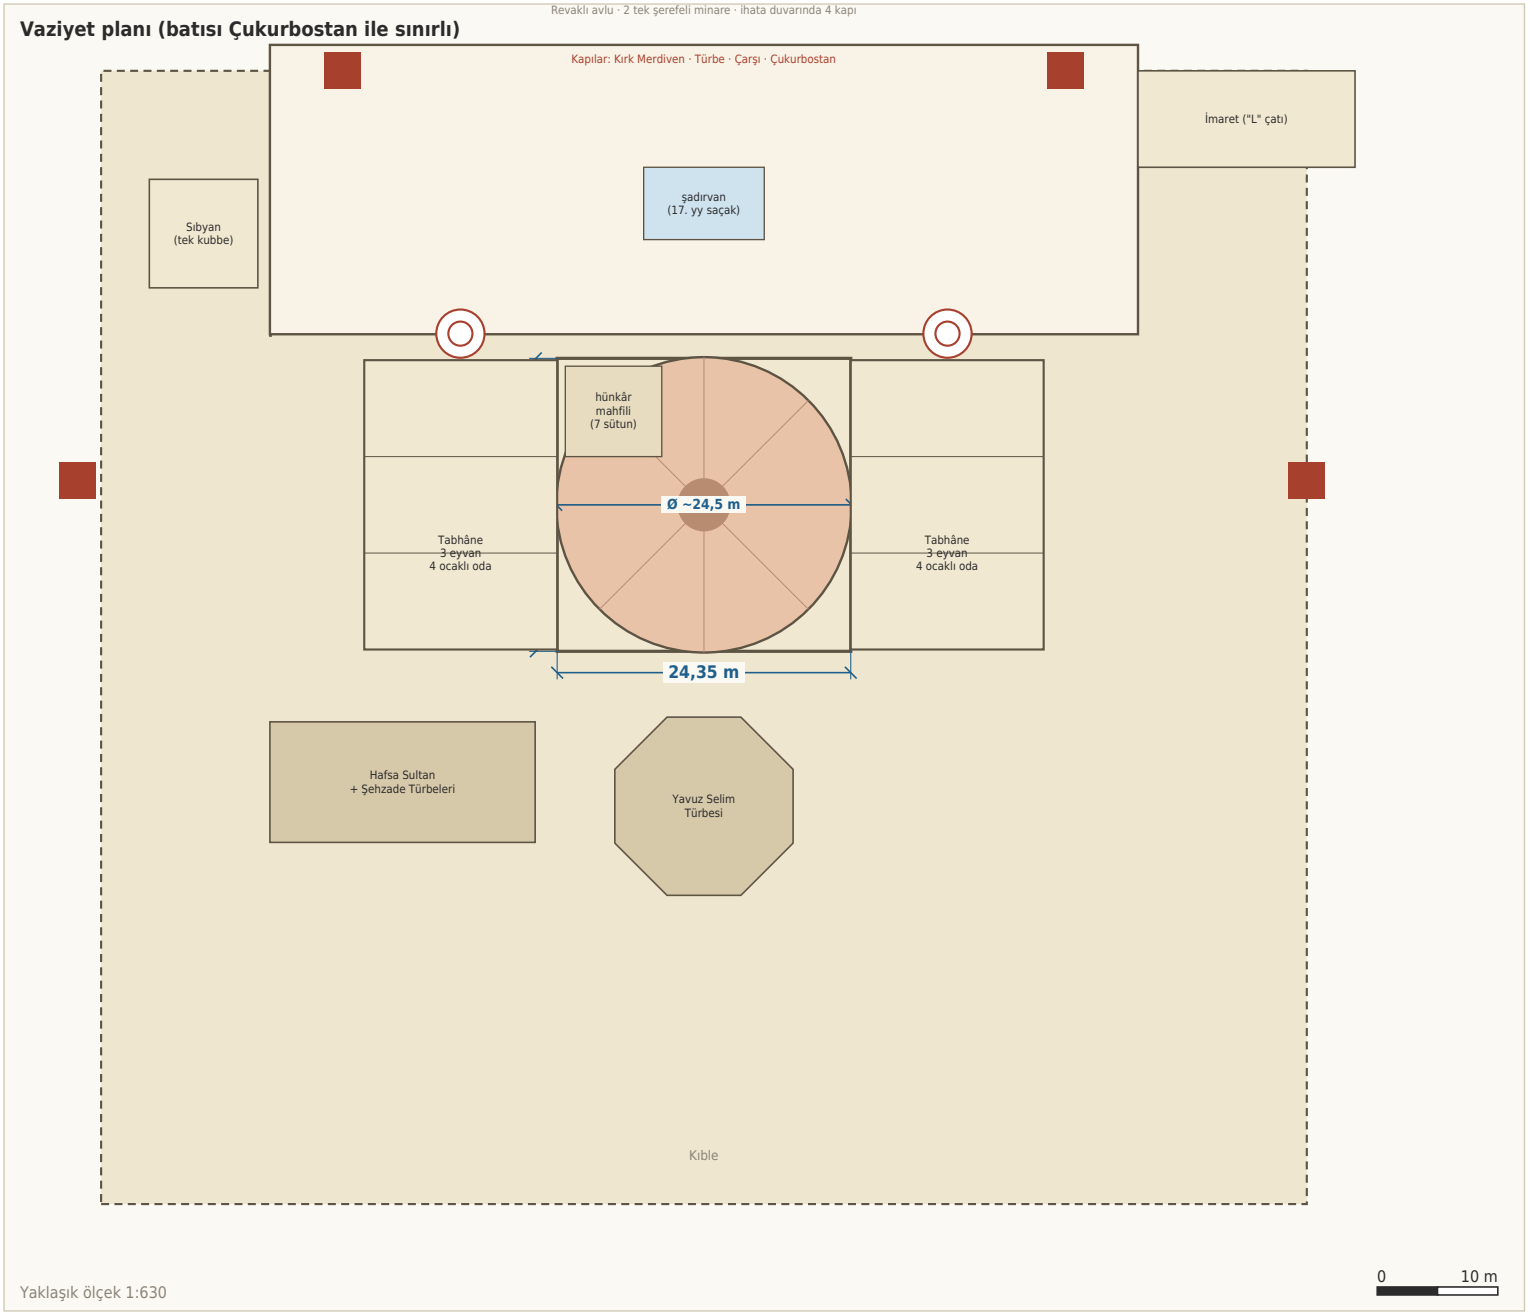

Ölçüler

Harim (kare)	**24,35 × 24,30 m**
Ana kubbe çapı	**~24,5 m**
Ana kubbe yüksekliği	**34,5 m**
Hünkâr mahfili	**7 sütunlu**
Tabhâne odası	**2 × 4 = 8 misafir odası**
Minare	**2 (tek şerefeli)**
İhata kapısı	**4**

Mimari

Pandantifli tek kubbe; iki yanda ana kütleye bitişik alçak, üçer eyvanlı ve dörder ocaklı odalı iki tabhâne (tabhaneli camilerin son örneği). Batısı tamamen Çukurbostan ile sınırlıdır.


Kıblede sekizgen, dilimli kubbeli Yavuz Sultan Selim Türbesi; Hafsa Sultan ve şehzade türbeleri; kuzeybatıda taş–tuğla almaşık Sıbyan Mektebi; kuzeyde "L" çatılı İmaret. 8 sütunlu şadırvan saçağı IV. Murad'un 17. yy ekidir, maketlenmemelidir.

Avlu ve ek yapı ölçüleri oransaldır †.

Rüstem Paşa Külliyesi (Tahtakale)

1555–1561 · Mimar Sinan · çarşı üzerinde yükseltilmiş cami

Zemin (çarşı) seviyesi – depo/dükkân altyapısı ve cami platformu (ölçeksiz)

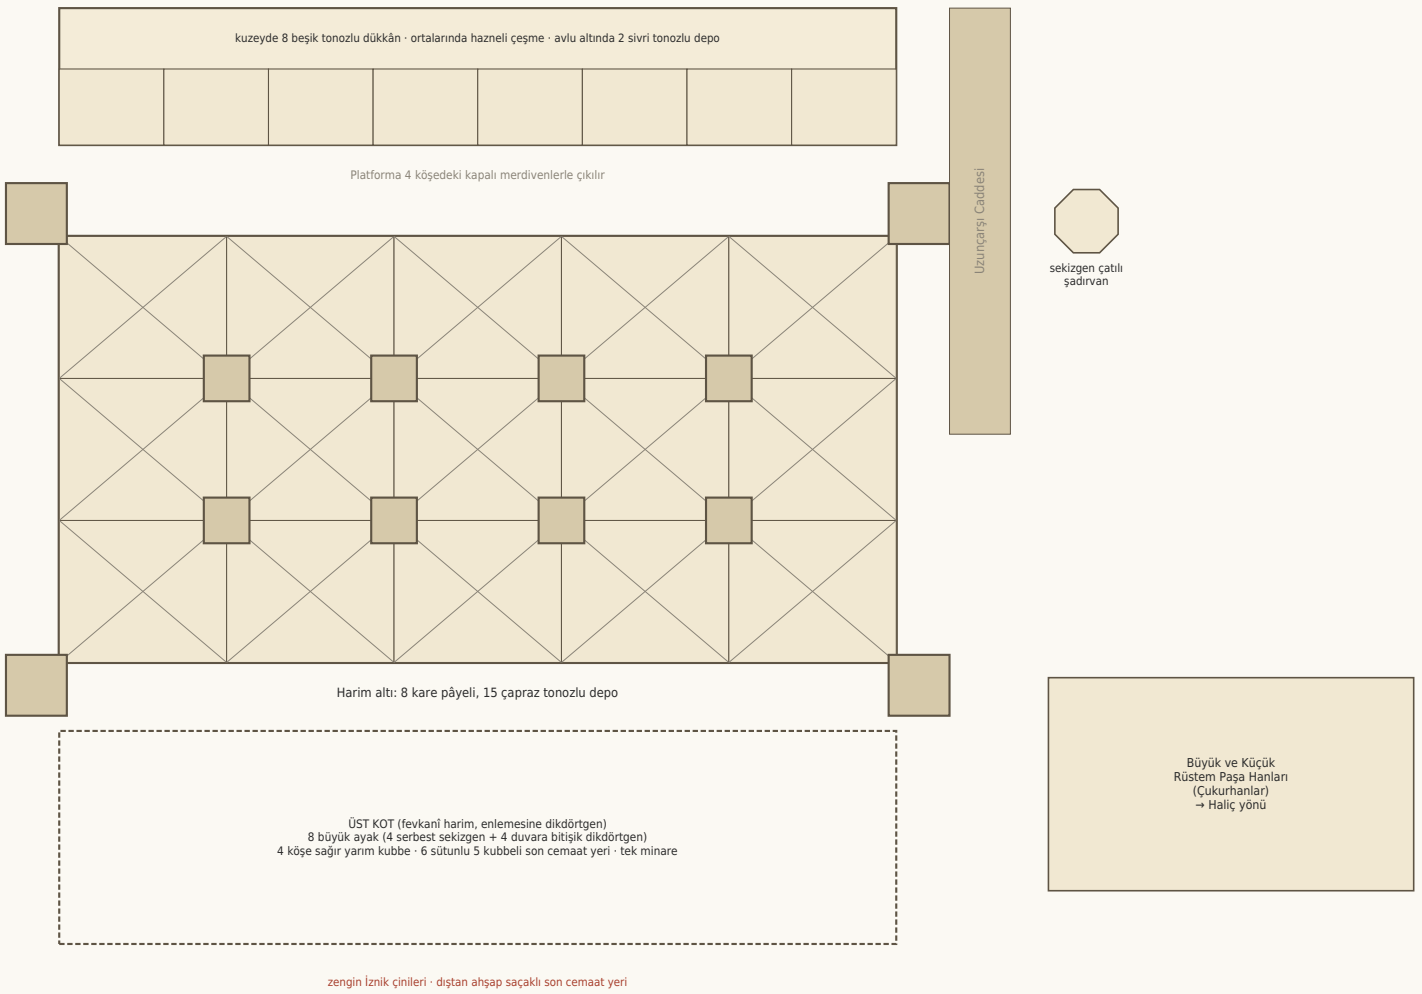

Ölçeksiz / şematik yerleşim

Sayısal veriler

Ayaklar	**8 (4 serbest + 4 duvarlı)**
Köşe yarım kubbe	**4 (sağır)**
Son cemaat yeri	**6 sütun / 5 kubbe**
Harim altı depo	**15 çapraz tonoz · 8 kare pâye**
Avlu altı depo	**2 sivri tonozlu**
Dükkân	**8 beşik tonozlu**
Minare	**1**


Yol seviyesinde alt yapı (depo + dükkân) üzerinde yükseltilmiş (fevkanî) platformda cami yer alır. Uzunçarşı Caddesi'nde sekizgen çatılı şadırvan, Haliç yönünde Rüstem Paşa Hanları bulunur.

Belgede metrik ölçü yoktur; şema sayısal düzeni (ayak, tonoz, kubbe adedi) gösterir †.

Fatih Külliyesi (Özgün 1470 Planı)

4. Tepe · 1463–1470 · Atik Sinan · 120.000 m² simetrik saha

Vaziyet şeması (1771 yapısı değil, Atik Sinan'ın ilk camisi)

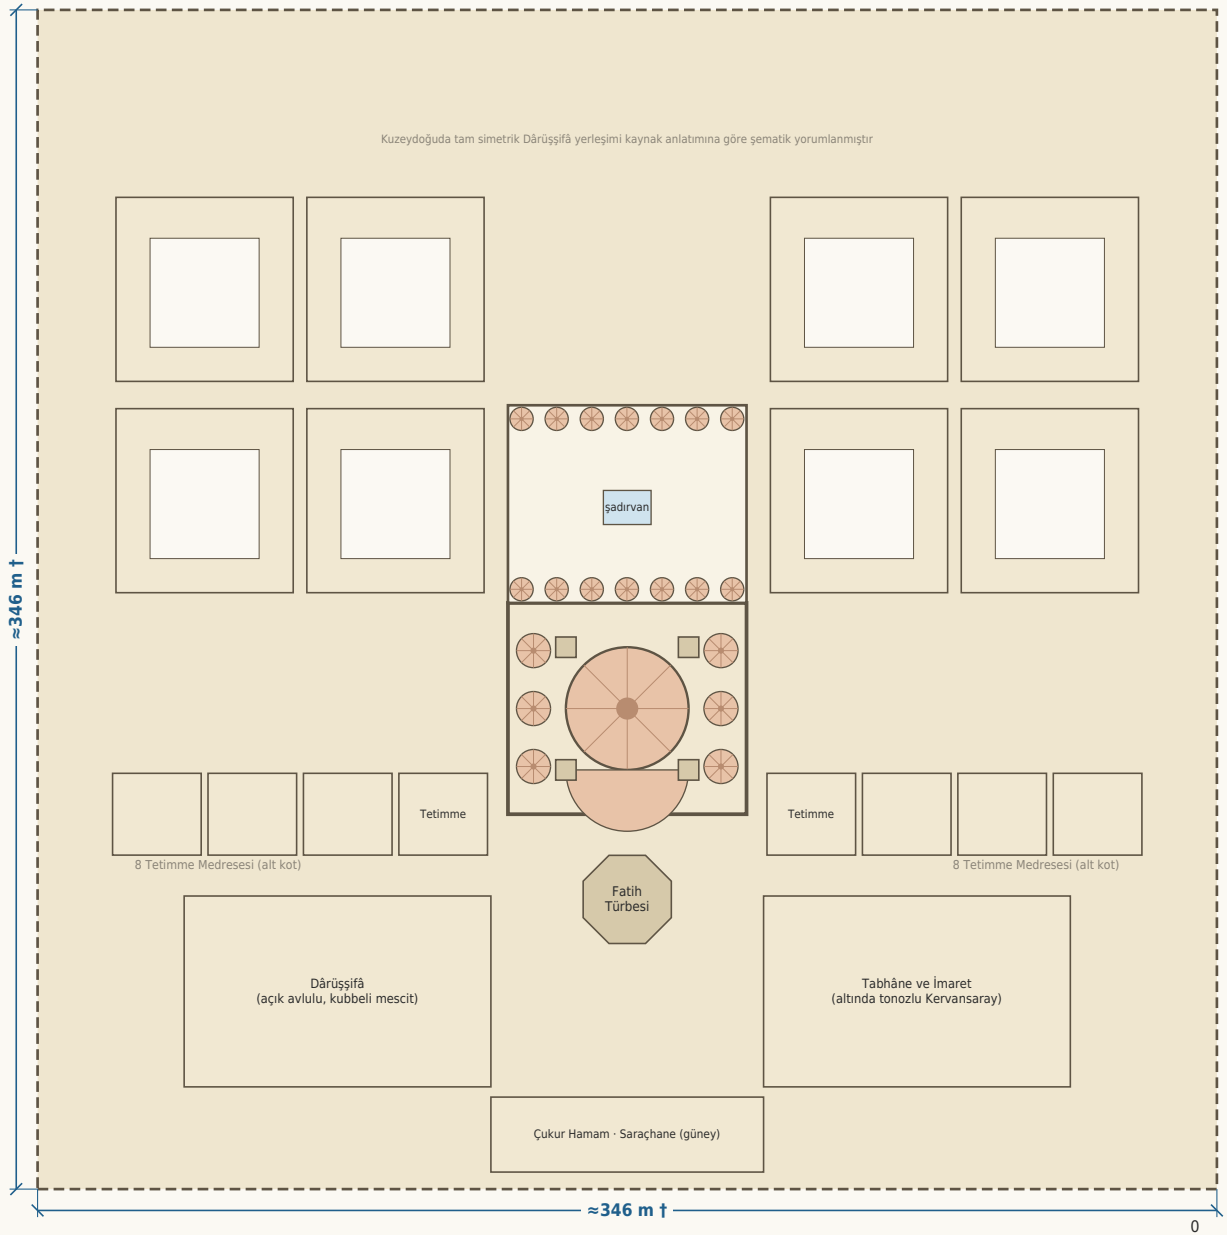

Yaklaşık ölçek 1:2.200

Ölçüler

Külliye alanı	**120.000 m²**
Eşdeğer kare kenarı	**≈346 m †**
Sahn-ı Seman Medresesi	**8 (4 + 4)**
Tetimme Medresesi	**8**
Sahn hücre sayısı	**19 hücre + 1 dershane / medrese**
Kütüphane (cami içinde)	**1.770 kitap**

Cami (1470)

İki sütun ve iki fil ayağı üzerinde büyük merkezî kubbe; yalnızca mihrap yönünde ileri taşkın bir yarım kubbe; iki yanda üçer küçük kubbeli yan sahınlar. 1509 ve 1557 deprem onarımları.


Ayrı kütüphane binası 18. yy ekidir. 1771 yapısı (dört yarım kubbeli) makette yer almaz.

Cami içi ölçüler belgede verilmemiştir; oransaldır †.

II. Bayezid Külliyesi

3. Tepe (Beyazıt Meydanı) · 1501–1507

Vaziyet planı (kuzey yukarı)

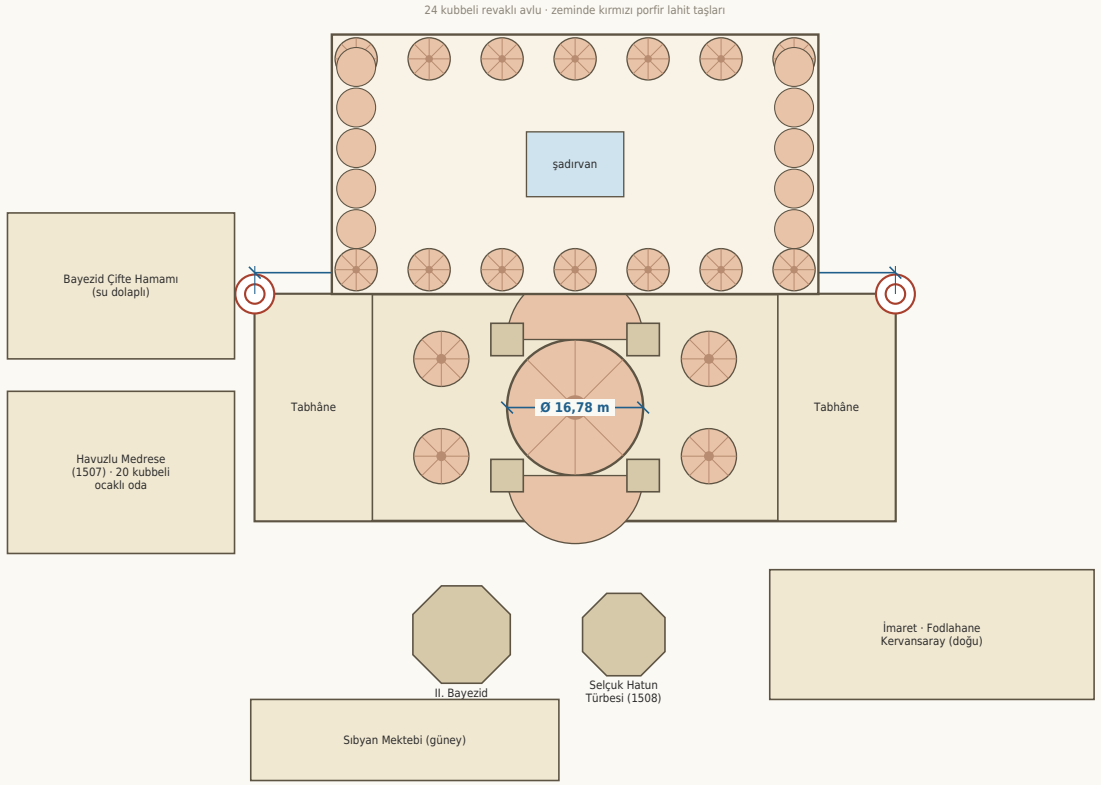

Yaklaşık ölçek 1:930

0 — 20 m

Ölçüler

Ana kubbe çapı	**16,78 m**
Kubbe kasnak penceresi	**20**
Yarım kubbe pencereleri	**7 + 7**
Minareler arası mesafe	**79 m**
Revaklı avlu	**24 kubbe**
Medrese	**20 kubbeli/ocaklı oda**

Mimari

4 ayak üzerinde ana kubbe, kuzey ve güneyde iki yarım kubbe, yanlarda kubbeli sahınlar ve iki yanda dışa taşkın tabhâneler; iki minare tabhânelerin dış uçlarındadır. Kıblede sekizgen II. Bayezid ve Selçuk Hatun türbeleri.


Darüşşifaya bitişik 18 odalı Tıp Medresesi Edirne külliyesine aittir, makete eklenmez.

Birim aralıkları oransaldır †.

Ayasofya-i Kebîr (Kanuni Dönemi) ve Haseki Hürrem Çifte Hamamı

Minare kuralı · 75 m uzunluğundaki hamam


Ayasofya – plan şeması: Kanuni devrin[illegible] fazla 3), payanda ve türbe yok

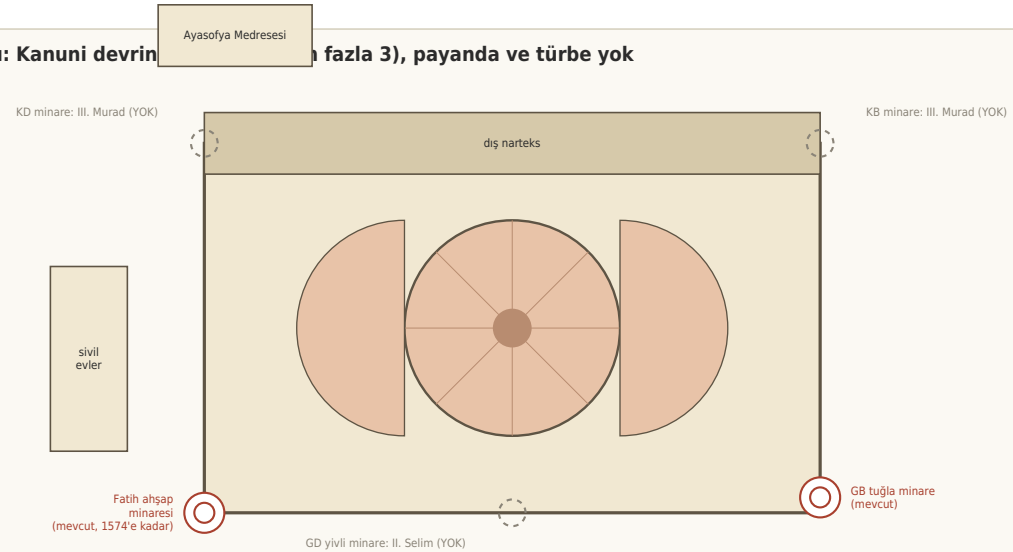

Kıble ↓ · iç mekânda mihrabın iki yanında Budin başkilisesinden getirilmiş (1526) iki tunç şamdan

Ölçeksiz / şematik yerleşim

Haseki Hürrem Sultan Çifte Hamamı – plan (uzunluk 75 m)

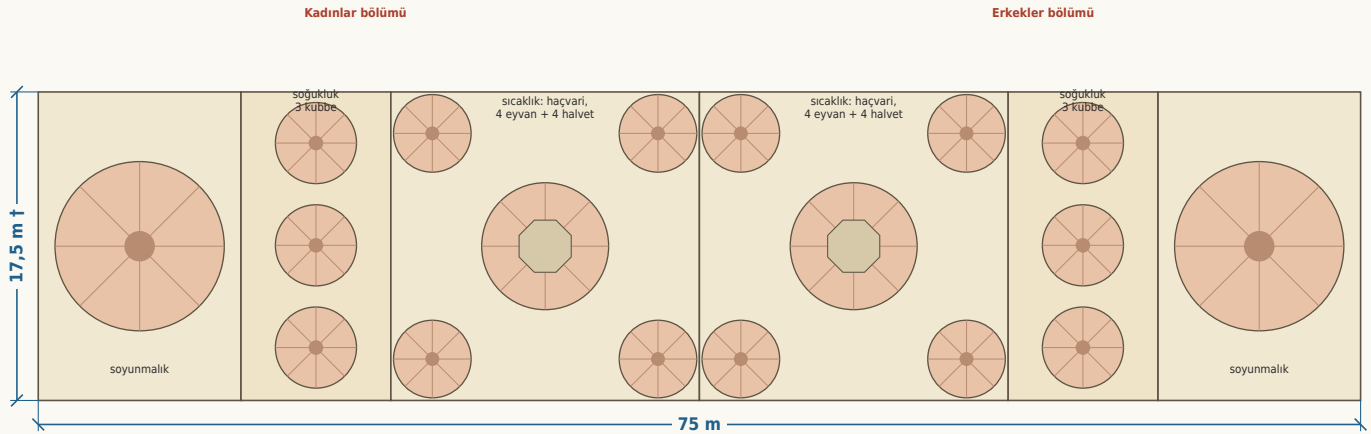

iki bölüm Türk hamam mimarisinde ilk kez aynı eksen üzerinde uç uca; ortada sıcaklıklar bitişik

Yaklaşık ölçek 1:430

0 — 10 m

Ayasofya (c. 1560)

Minare sayısı	**2 (en fazla 3)**

Mevcut: batı yarım kubbe yanındaki güney baskı kulesinde Fatih'in ahşap minaresi (1574 tamirine kadar) ve güneybatı köşede tuğla minare.

Yok: güneydoğu yivli minare (II. Bayezid veya daha çok II. Selim, Sinan), kuzeydeki iki minare (III. Murad), Sinan payandaları ve sultan türbeleri (II. Selim sonrası), 1742 I. Mahmud İmareti.

Yapıya bitişik sivil evler ve kuzeyde Fatih'in Ayasofya Medresesi (altmış akçeli) vardır.

Haseki Hamamı


Toplam uzunluk	**75 m**
Her bölümde	**kare kubbeli soyunmalık**
	3 kubbeli soğukluk
	4 eyvan + 4 kubbeli halvet

Sağda helalar, solda usturalık, ortada sekizgen göbek taşı. Genişlik oransaldır †. Konum: Ayasofya ile Atmeydanı arası.

İbrahim Paşa Sarayı ve Eski Saray (Sarây-ı Atîk)


Atmeydanı'nın batısı · 3. Tepe

İbrahim Paşa Sarayı – vaziyet (cephe 140 m, dört avlu, ölçeksiz iç düzen)

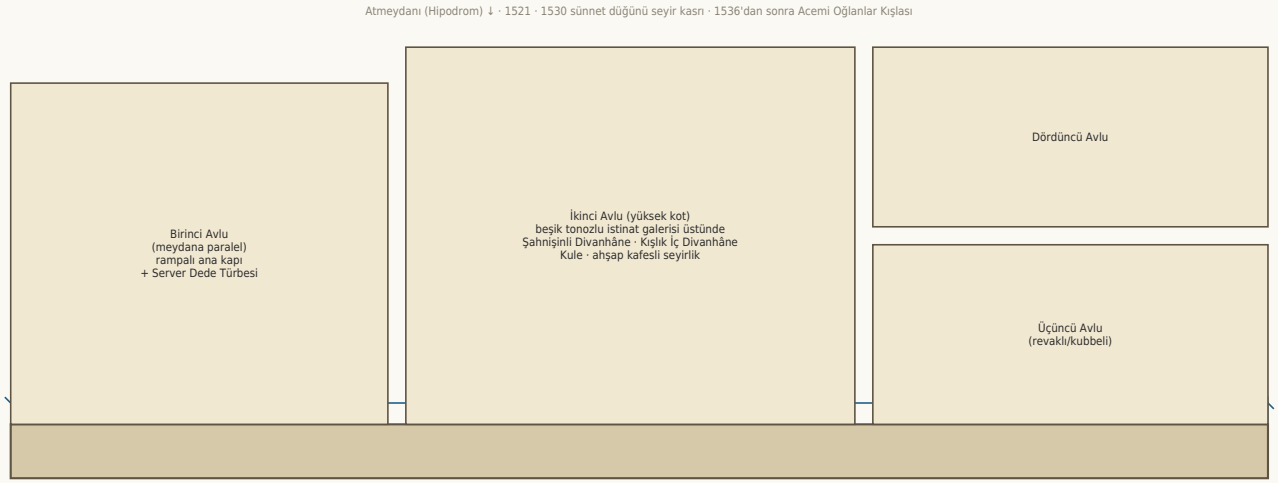

Yaklaşık ölçek 1:840

Eski Saray – çift sur şeması (burçsuz, kulesiz, hendeksiz; mavi kurşun kaplı)

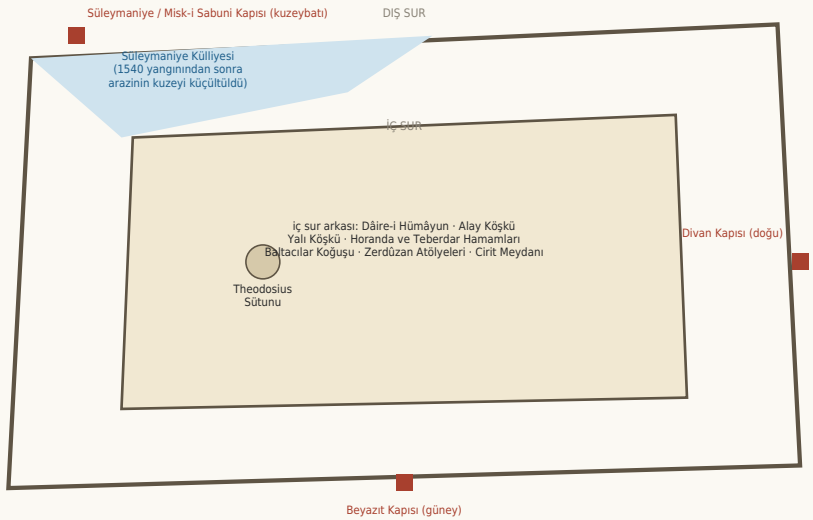

Ölçeksiz / şematik yerleşim

İbrahim Paşa Sarayı

Cephe genişliği	**140 m**
Avlu sayısı	**4**
Yapım	**1521 (genişletme)**

Eğimli arazide meydana bakan beşik tonozlu istinat galerisinin (bodrumu dükkân ve ahır) üzerinde yüksek kotlu İkinci Avlu yer alır; bugün Türk ve İslam Eserleri Müzesi olan tek sağlam avludur.

Eski Saray


Sur çevresi (kaynaklarda)	**1–2 mil / 12.000 arşın**
Kapı sayısı	**3–4**
Yangın	**5 Şubat 1540**

Burçsuz, kulesiz, hendeksiz yüksek taş sur; üzeri mavi kurşun. İç içe iki sur; Lorichs'in 1559 çiziminde surlar Haliç yönünde üçgen yapar. Tüm yerleşim ölçeksizdir.

Topkapı Sarayı – Genel Vaziyet Şeması

Sarây-ı Cedîd-i Âmire · 700.000 m² · dört avlu, üç anıtsal kapı, Harem

Genel şema (kuzey yukarı; Haliç kuzeyde, Marmara güneyde, Sarayburnu doğuda) – ölçeksiz

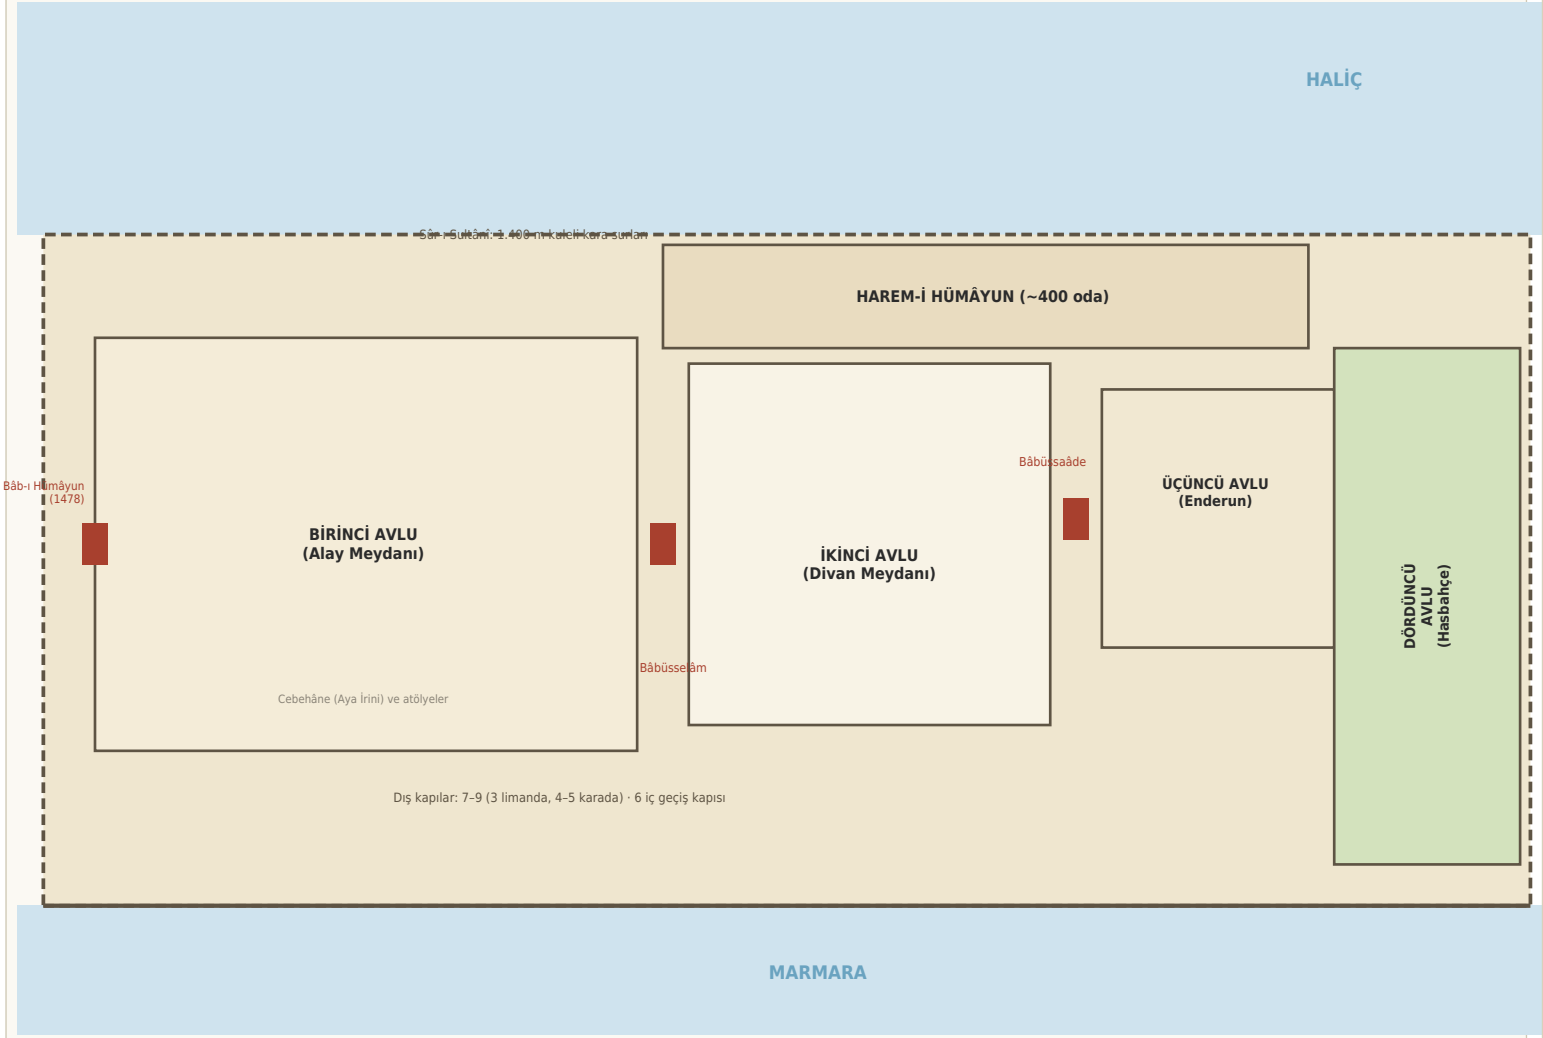

Ölçeksiz / şematik yerleşim

Genel ölçüler

Saray alanı	**700.000 m²**
Kara surları (Sûr-ı Sultânî)	**1.400 m**
Dış kapı	**7–9**
İç geçiş kapısı	**6**
Harem oda sayısı (nihai)	**~400**
Avlu sayısı	**4**

Kapı dizisi

Bâb-ı Hümâyun (Saltanat Kapısı, 1478) → Birinci Avlu → Bâbüsselâm (Ortakapı) → İkinci Avlu → Bâbüssaâde (Akağalar Kapısı) → Üçüncü Avlu (Enderun) → Dördüncü Avlu / Hasbahçe.

Çıkarılacak sonraki yapılar

Bağdat Köşkü (1639), Revan Köşkü (1635), Seferli Koğuşu (1635), III. Ahmed Kütüphanesi (1719), Mecidiye Köşkü, Sofa Köşkü, İftariye (1640).

Şema, avlu sırasını ve ilişkileri gösterir; avlu boyutları belgede verilmediğinden ölçeksizdir.

Birinci Avlu ve Bâb-ı Hümâyun


Alay Meydanı · zemin: sıkıştırılmış toprak (minyatürde sarı)

Birinci Avlu planı (Bâb-ı Hümâyun'dan Bâbüsselâm'a bakış; kuzey yukarı) – ölçeksiz



Ölçeksiz / şematik yerleşim

Bâb-ı Hümâyun – ön görünüş (şematik)

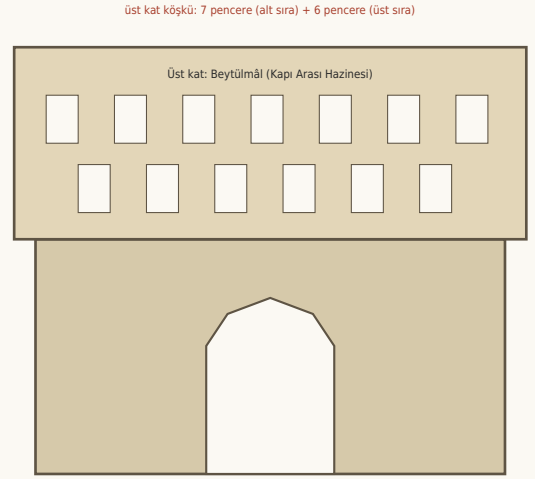

Ölçeksiz / şematik yerleşim

Bâb-ı Hümâyun

Yapım	**1478**
Kat sayısı	**2 (köşk-kapı)**
Üst kat pencereleri	**7 alt sıra / 6 üst sıra**
Nöbetçi odası	**3 (asma kat)**
Beytülmâl miras saklama	**7 yıl**

Üst kat köşkü 1867 yangınında yıkılmıştır ancak Kanuni devri maketinde mutlaka yer almalıdır.

Avlu içeriği


Sağ (Marmara) taraf: Dış Karakol, Enderun Hastanesi, Su Dolabı Ocağı, fırınlar, Deâvî Kasrı. Sol (Haliç) taraf: Aya İrini/Cebehâne, Darphâne, Ambarhâne, Odun Ambarı, Hasırcılar, Acemiler Ocağı, Nakkaşhâne, Mimarlar Ocağı, Mehterhâne, ehl-i hiref atölyeleri.

Plan yerleşimi belgedeki yön tariflerinin şematik yorumudur; mesafeler ölçeksizdir.

İkinci Avlu (Divan Meydanı)

Kubbealtı, Dış Hazine, Has Ahırlar, Matbah-ı Âmire

Avlu planı (Bâbüsselâm solda, Bâbüssaâde sağda; kuzey yukarı) – ölçeksiz

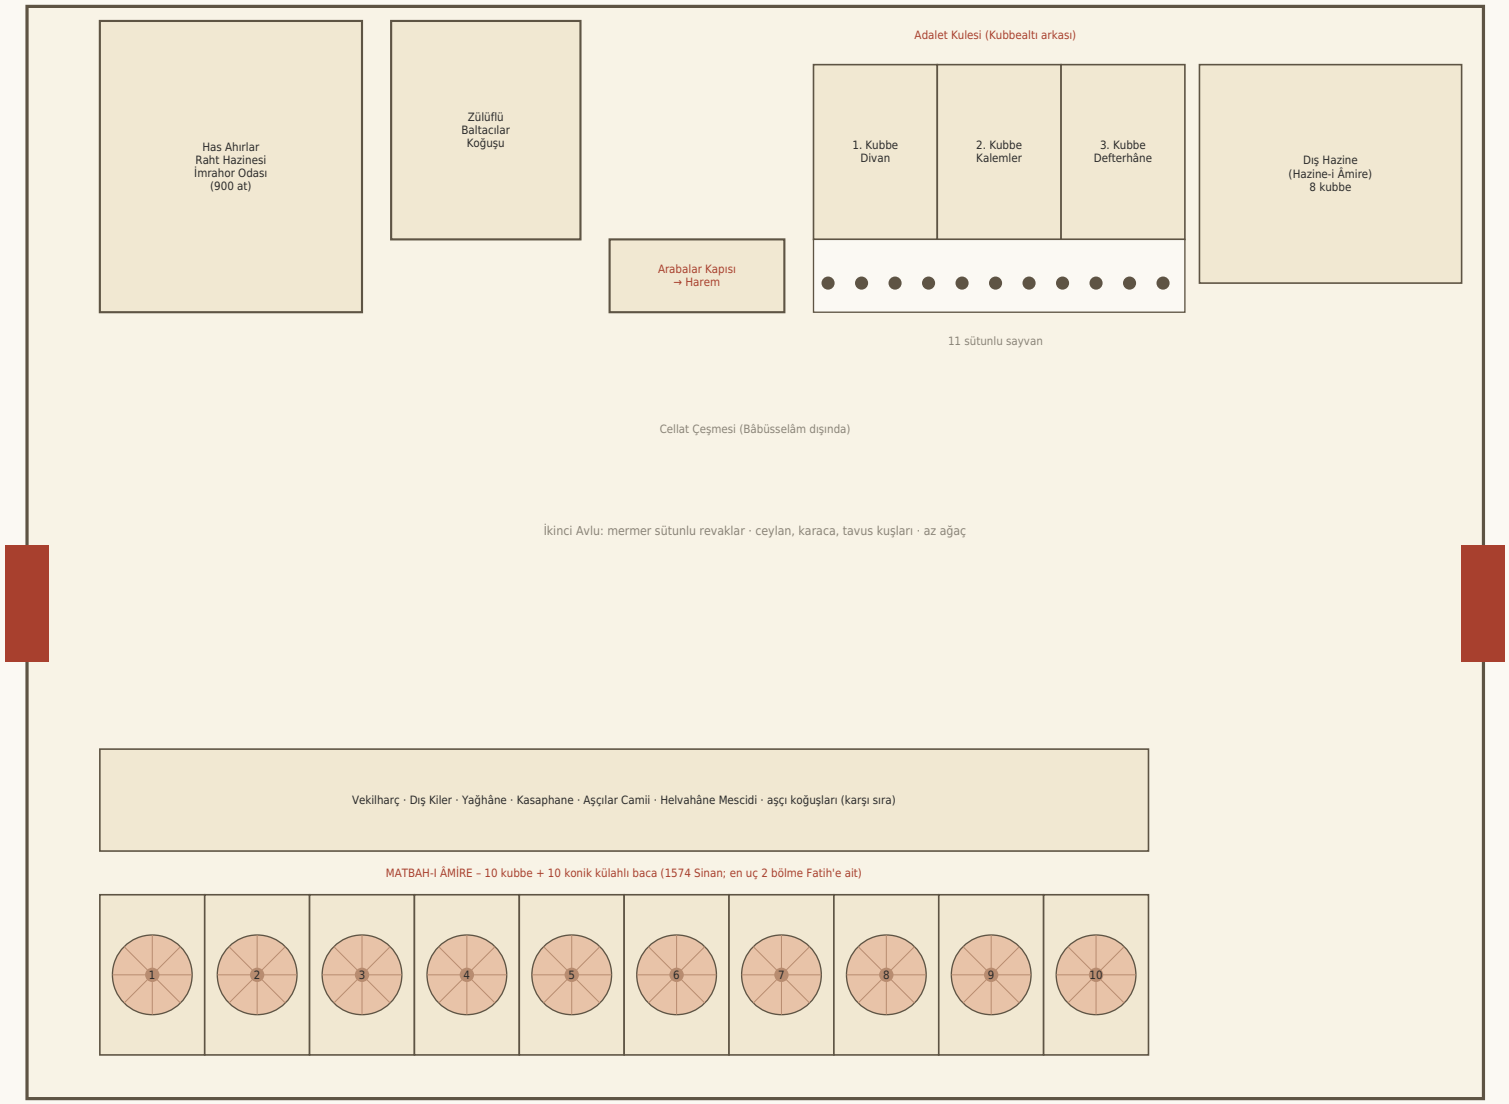

Ölçeksiz / şematik yerleşim

Kubbealtı

Kubbe sayısı	**3**
Sayvan sütunu	**11 (yeşil porfir + beyaz mermer)**
Divan toplantısı	**haftada 4 gün**

Dış Hazine

Kubbe	**8**

Has Ahırlar

1. ahır	**200 seçkin at**
2. ahır	**40–50 padişah/ağa atı**
Toplam at	**900 (40 şecereli + 300–400 koşu)**

Saray mutfakları

Bölme / kubbe / baca	**10 / 10 / 10**


1. Has + Kuşhâne, 2. Valide, 3. Haseki/Kadınlar, 4. Kapıağası, 5. Divan, 6. Ağayân, 7. Enderun Gılmân, 8. Hizmetkârlar/Dârüssaâde, 9–10. Helvahâne ve Reçelhâne.

Numaralandırma belgedeki güney→kuzey sırasının şematik karşılığıdır; yerleşim ölçeksizdir.

Arz Odası (Bâbüssaâde'nin karşısı) – Plan ve Ölçüler

Üçüncü Avlu · taş-tuğla almaşık örgülü kâgir köşk

Plan (kuzey yukarı)

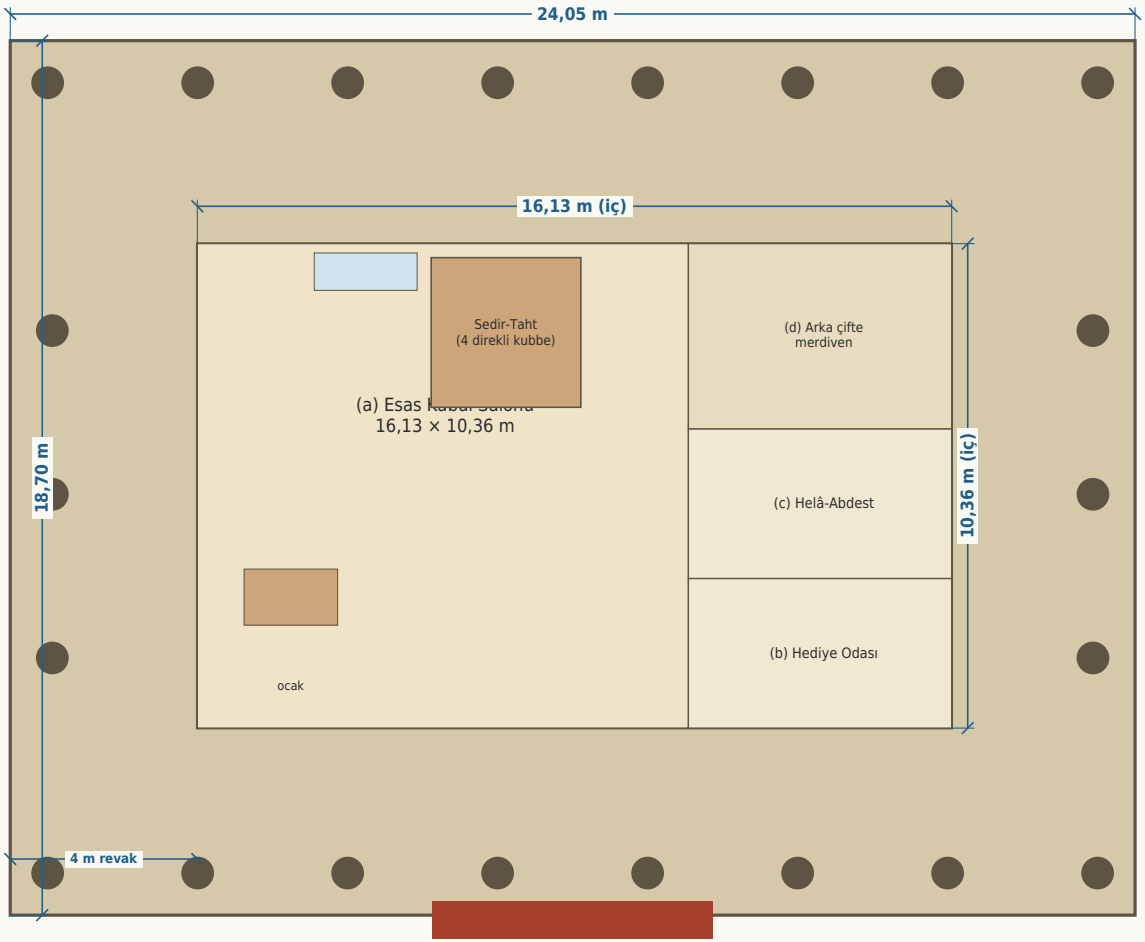

Bâbüssaâde'ye bakan cephe: 2 kapı + Mâruzat Penceresi · sağda Kanuni çeşmesi

Yaklaşık ölçek 1:160

0 5 m

Ölçüler

Dış boyut	**24,05 × 18,70 m**
İç kapalı mekân	**16,13 × 10,36 m**
Revak dehlizi genişliği	**4 m**
Sütun (bugün)	**22 (20 breş + 2 beyaz)**
Örtü	**geniş saçaklı ahşap çatı + gizli kubbe**

Kanuni devrinde revak mermer sütunludur (Fatih devrinde ahşap direkli); bugünkü sütun düzeni ve taht kubbesi III. Mehmed devri (1597–98) yenilemesidir.

İç mekân

Esas salonda sol köşede dört ince direkli kubbeli, mücevher kakmalı Sedir-Taht; arka çıkış kapısı kenarında su şırıltısıyla gizli görüşmeleri bastıran İç Çeşme; mermer çerçeveli dört dolap nişi; iki nişin ortasında yaldızlı tunç davlumbazlı büyük ocak.


Arkada avlu eğimli olduğundan arka dehlizden avluya çifte merdivenle inilir. Arkasındaki III. Ahmed Kütüphanesi (1719) yoktur; yerinde Havuzlu Köşk vardır.

İç bölüm paylaşımları ve sütun konumları şematiktir †.

Has Oda Kasrı (Hırka-i Saâdet / Mukaddes Emanetler Dairesi)

Üçüncü Avlu kuzeybatı köşesi · Harem'e bitişik


Üst kat planı (şematik oda düzeni)

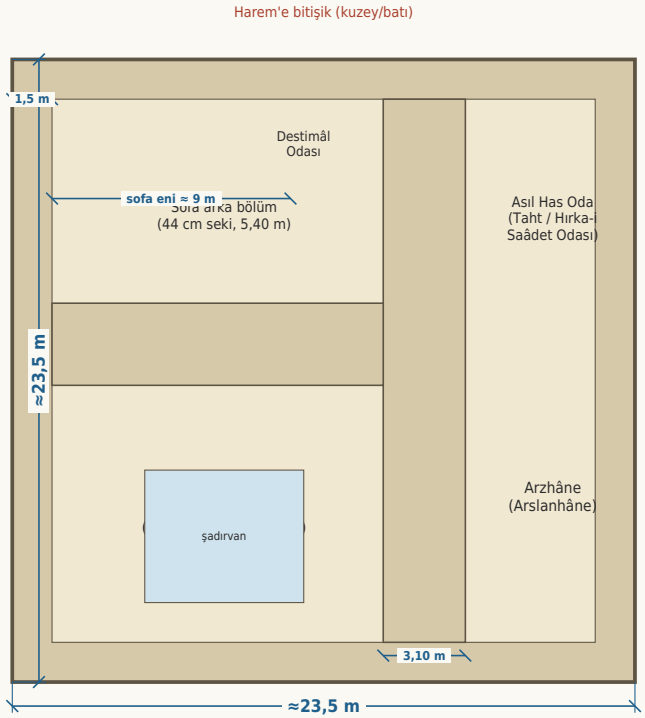

Yaklaşık ölçek 1:290

0 5 m

Kesit (şematik): bodrum – ana kat – kubbeler

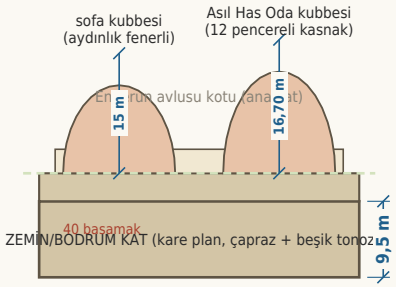

Yaklaşık ölçek 1:940

0 20 m

Ölçüler

Dış boyut	≈23,5 × 23,5 m
Dış duvar kalınlığı	1,5 m
İç eksen duvarı	3,10 m
Bodrum kotu	9,5 m aşağıda
Merdiven	40 basamak
Örtü	4 kubbe
Sofa kubbeleri yüksekliği	15 m
Asıl Has Oda kubbesi	16,70 m
Sofa genişliği / seki	≈9 m / 44 cm × 5,40 m
Destimâl duvarı	1,90 m

Odalar

Şadırvanlı Sofa (iki kubbeli giriş salonu, kıble göstergeli), Arzhâne (4 pencereli kasnak, İznik çinili; Mukaddes Emanetler Hazinesi'ne geçiş), Asıl Has Oda (en yüksek kubbe; padişah tahtı ve Hırka-i Saâdet, Sancak-ı Şerif), Destimâl Odası.


IV. Murad kubbe/çini ve 11 kubbeli Haliç revağı 17.–19. yy ayrıntılarıdır; Kanuni devri maketinde sade bırakılır.

Oda içi bölüşüm şematiktir †.

Üçüncü Avlu (Enderun-ı Hümâyun) – Yerleşim Şeması

Koğuşlar, hazine, Arz Odası, Has Oda ve Fatih Köşkü

Üçüncü Avlu planı – belgedeki yön tariflerine göre şematik (kuzey yukarı) – ölçeksiz

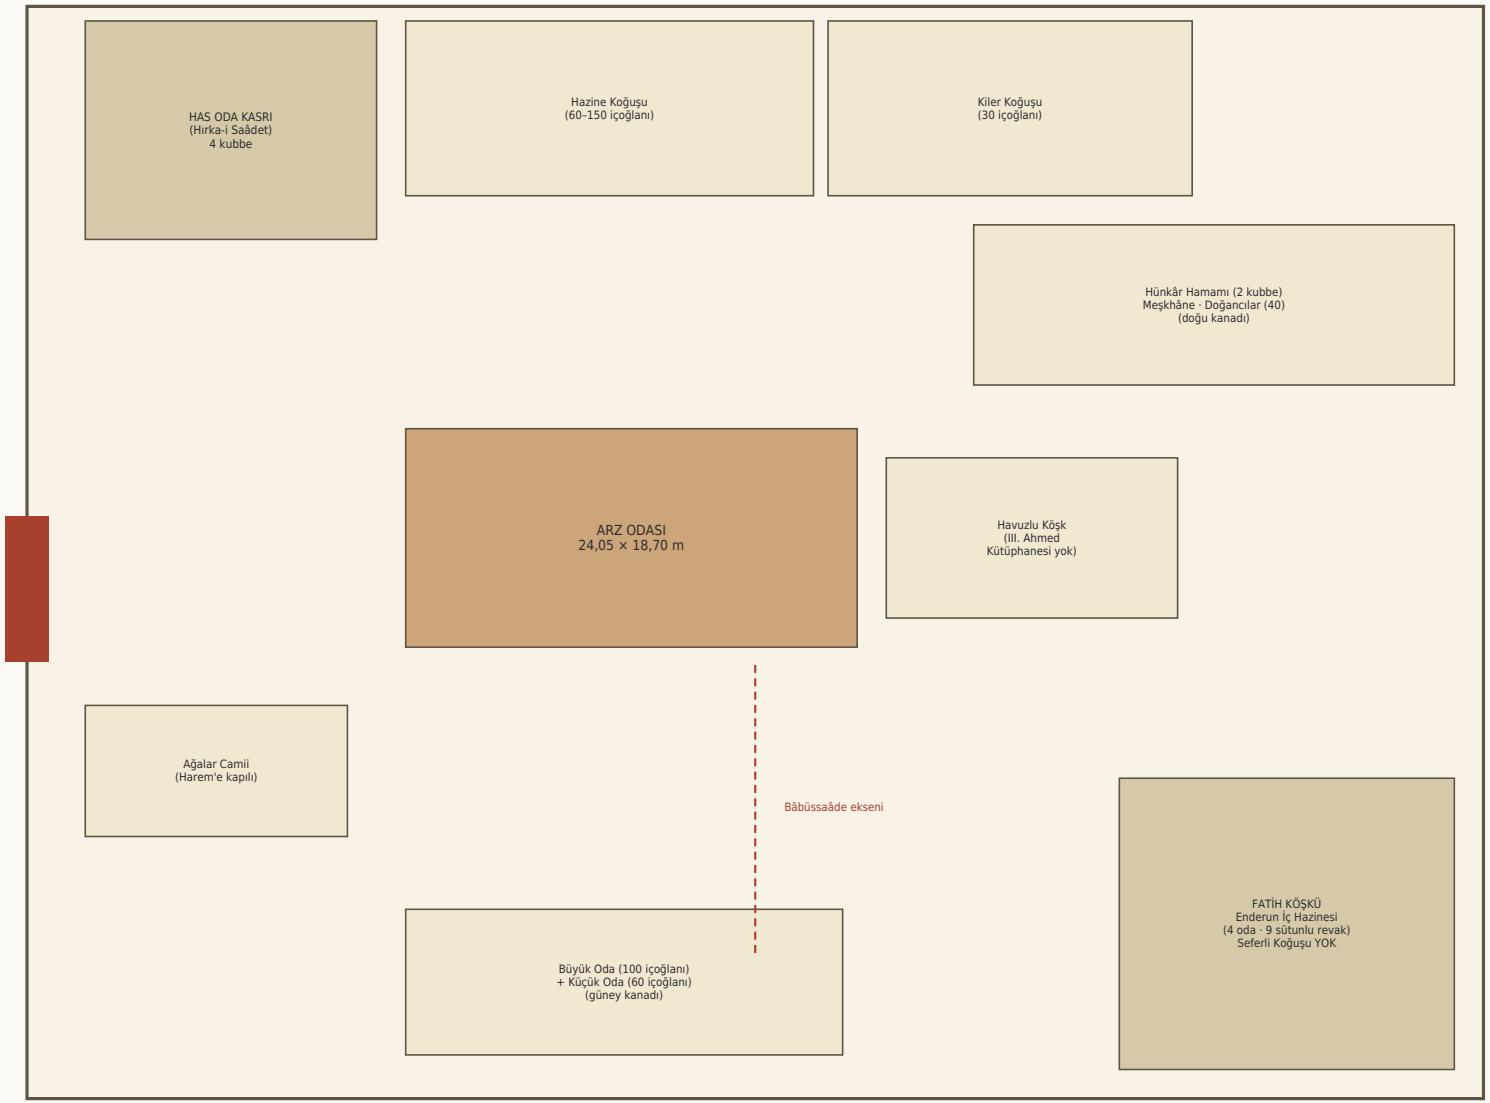

Ölçeksiz / şematik yerleşim

Kadro / sayılar

Büyük Oda	**100 içoğlanı**
Küçük Oda	**60 içoğlanı**
Doğancılar Koğuşu	**40 kişi**
Hazine Koğuşu	**60–150 içoğlanı**
Kiler Koğuşu	**30 içoğlanı**

Maket uyarıları

Seferli Koğuşu 1635'te IV. Murad tarafından kurulmuştur; Kanuni devrinde o kanatta Hünkâr Hamamı, Meşkhâne ve Doğancılar Koğuşu yer alır.

Arz Odası'nın arkasındaki III. Ahmed Kütüphanesi (1719) yerine Havuzlu Köşk modellenmelidir.


Yön tarifleri belgede birbirine tam uyumlu olmadığından yerleşim yorumsaldır †.

Temsili şema. Boyutlar belgedeki verilerden alınmıştır; † işaretli değerler türetilmiş / oransal / kaynakta bulunmayan varsayımdır. Ölçek A4 yatay %100 yazdırmada geçerlidir.

Üçüncü ve Dördüncü Avlu Köşkleri – Plan Şemaları


Fatih Köşkü · Çinili Köşk · Sünnet Odası · Hekimbaşı Kulesi

Fatih K

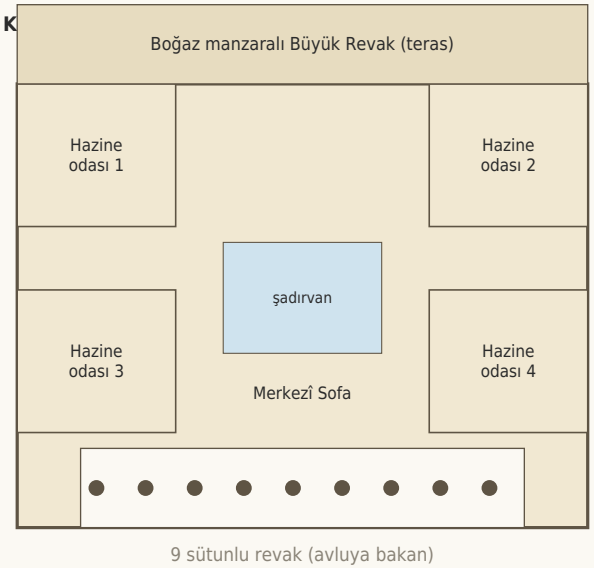

Yaklaşık ölçek 1:480

Çinili Köşk (1472) – kat pla

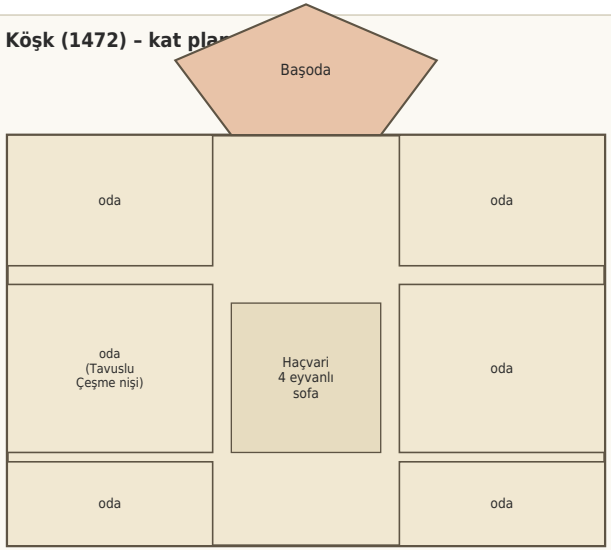


Yaklaşık ölçek 1:400

Sünnet Odası (Yazlık Kasır)



Yaklaşık ölçek 1:480

Hekimbaşı (Başlala / Taş) Kulesi – kare plan

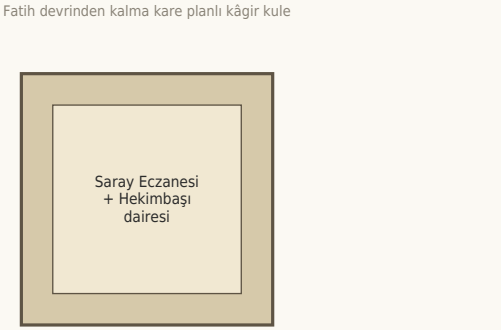

Yaklaşık ölçek 1:480

Fatih Köşkü

Yapım	**1463 (iki katlı)**
Revak	**9 sütunlu düz tavan**
Ana hazine odası	**4**

Marmara'ya hâkim sarp yamaçta; 16. yy'da padişahın şahsi hazinesi (Enderun İç Hazinesi), kapısı Yavuz Selim mührüyle mühürlü.

Çinili Köşk

Yapım	**1472**

Haçvari dört eyvanlı sofa, Boğaz ve Haliç'e doğru beş köşeli kubbeli başoda; solda Tavuslu Çeşme nişi.

Sünnet Odası

Çini panolar	**1,25 m yekpare**

Kanuni devrinde yazlık kasırdır; 1640'ta Sultan İbrahim iki odaya bölmüştür.

Çıkarılacak


Revan Köşkü (1635), Bağdat Köşkü (1639), İftariye (1640), Sofa ve Mecidiye köşkleri.

Bu sayfadaki oda ölçüleri belgede verilmediğinden oransaldır †.

Harem-i Hümâyun – Altı Bölge Şeması

Kanuni / Hürrem Sultan çekirdeği ve nihai yerleşim

Bölge ilişkileri (kuzey yukarı; Haliç'e bakan taraf solda) – ölçeksiz

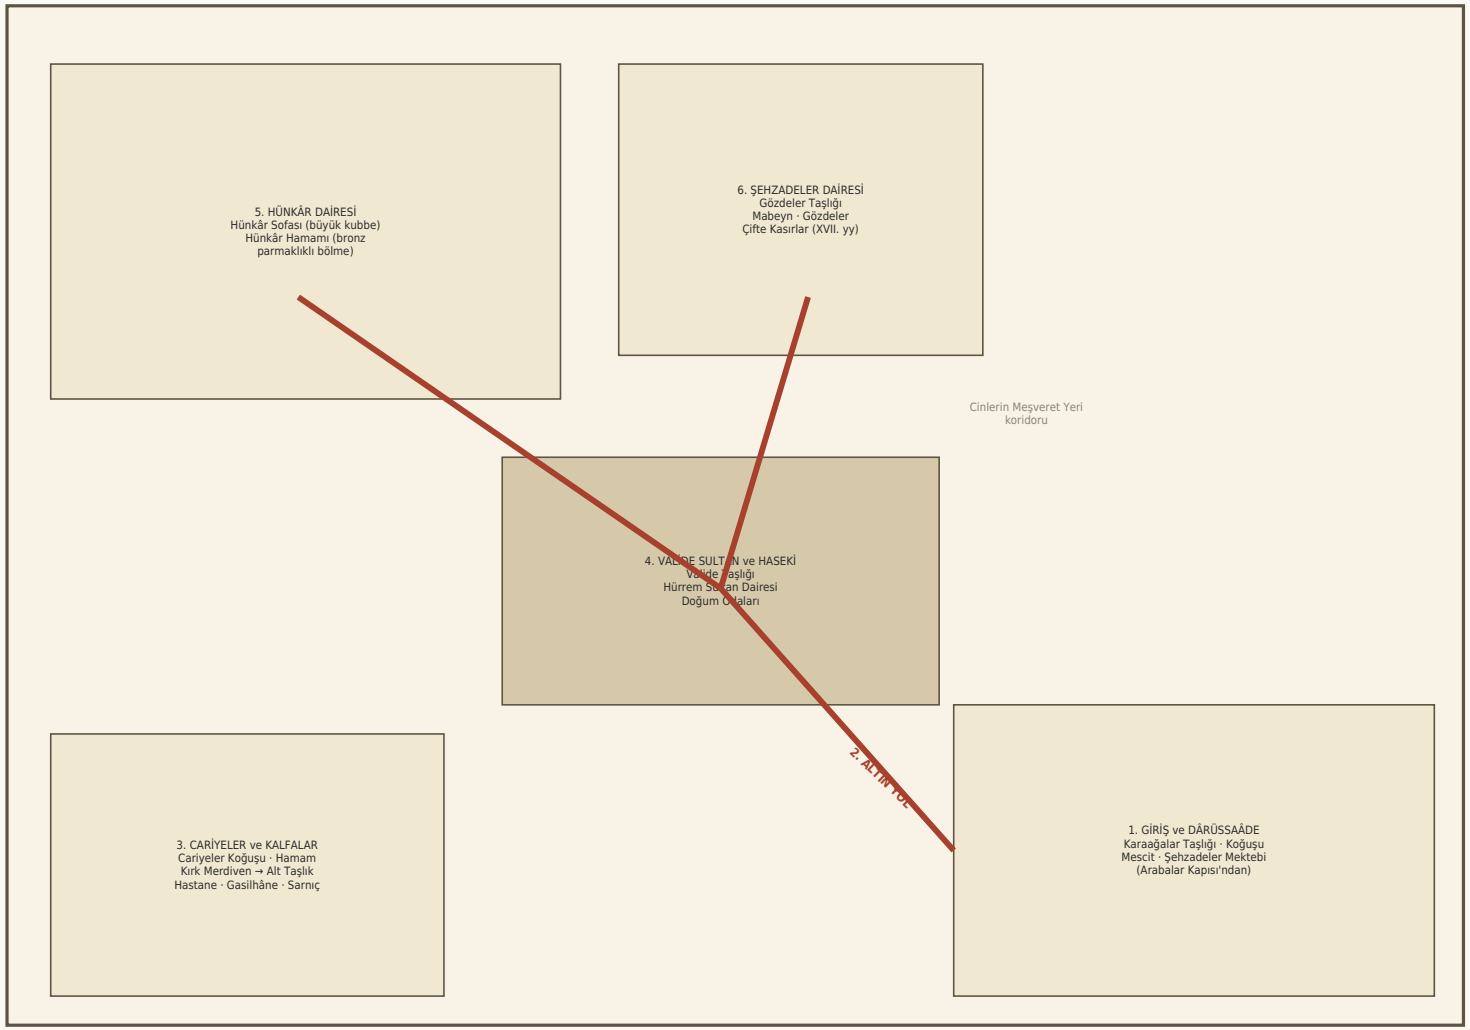

Ölçeksiz / şematik yerleşim

Genel

Nihai oda sayısı	**~400**
Taşınma	**1540/41 yangınından sonra**
Tamamlanma	**1578 (Sinan, Davud Ağa)**

Fatih devrinde Harem halkı Eski Saray'dadır; Topkapı'da yalnız küçük bir Kızlar Sarayı vardır (Matrakçı 1537: Adalet Kulesi önünde az pencereli dikdörtgen bina).

Kanuni devri çekirdeği

Taşlık–koğuş çekirdeği: Karaağalar Taşlığı, Cariyeler Koğuşu, Valide Taşlığı ve 16. yy Haseki dairesi (duvar içi mermer sütunlar, revzen + çift kanatlı kafes, kesme taş ocak).

Sonradan eklenenler (makete konmaz)


III. Murad Has Odası (1578), Hünkâr Sofası'nın III. Osman Rokoko yenilemesi, I. Ahmed Köşkü, III. Ahmed Yemiş Odası (1705), III. Osman Köşkü, Mihrişah Valide Odası (18. yy), Veliaht Dairesi (17. yy).

Altı bölge yerleşimi ilişkileri gösteren şemadır; plan ölçeksizdir †.

Büyük Çarşı (Kapalıçarşı) – Bedestenler ve Çifte Kepenkli Dükkân

Kanuni devrinde sokaklar henüz tonozlu değil: ahşap çatı/tente


Cevâhir Bedesteni – plan (1.008 m²)

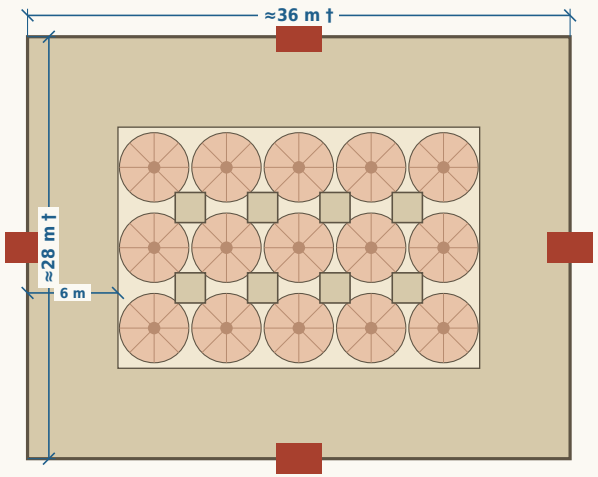

Yaklaşık ölçek 1:500

15 kubbe · 8 pâye · 4 demir kapı · 118 sanduka · 28 mahzen


Sandal Bedesteni – plan (20 kubbe)

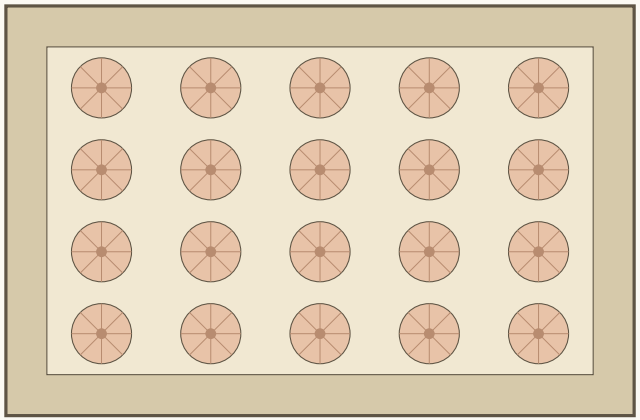

20 kubbe · ~300 demir kasa · ipekli (harîr) ve sandal kumaşları

Ölçeksiz / şematik yerleşim

Çarşı sokağı enine kesiti (Kanuni devri): ahşap saçak / tente + çifte kepenk

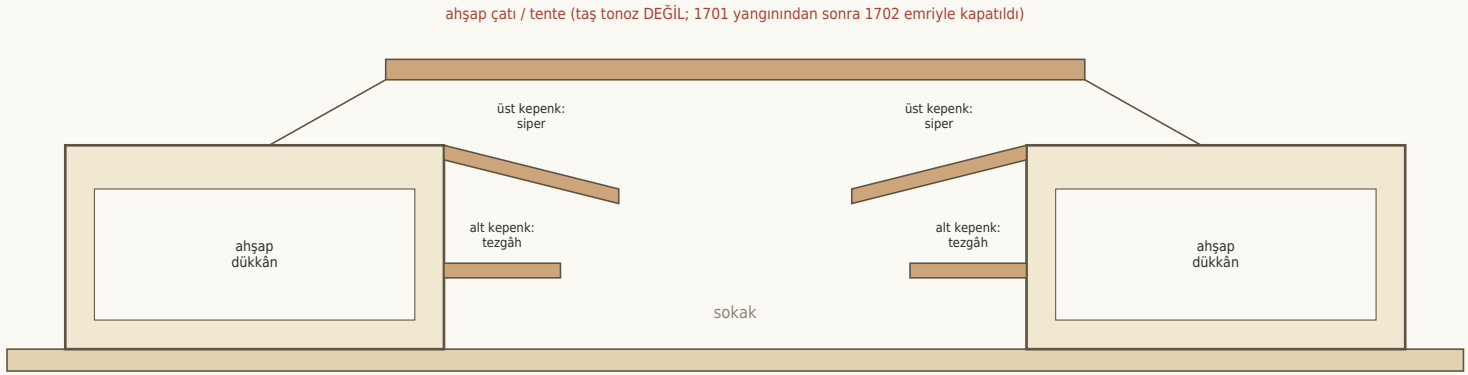

Ölçeksiz / şematik yerleşim

Cevâhir (İç) Bedesten

Alan	**1.008 m²**
Duvar kalınlığı	**6 m**
Pâye (ayak)	**8**
Kubbe	**15 (dıştan 23 görünür)**
Demir kapı	**4**
Sanduka (dolap)	**118**
Mahzen	**28 (4 köşe + 24 duvar içi)**
Eşdeğer boyut (türetilmiş)	**≈36 × 28 m †**

Her sabah duâcı bölükbaşı duası ile ticaret başlar; yüksek değerli mallar yalnız Perşembe müzayede edilir.

Sandal (Yeni) Bedesten

Kubbe	**20**
Demir kasa	**~300**

Dükkânlar


1489 Ayasofya Vakfı dükkân	**641 (76 kuyumcu, 50 terzi/keçeci…)**
Fatih vakfiyesi (bab)	**849**

Sokaklar: Altuncular, Aynacılar, Halıcılar, İplikçiler, Terziler, Saraçlar. 1515, 1539 ve 1546 yangınlarında ahşap dükkânlar yanmış, yalnız bedestenler kalmıştır.

Elçi Hanı (Divanyolu – Çemberlitaş Karşısı)

Dernschwam'ın 1553–55 ölçümleri · 16. yy han mimarisinin en eksiksiz modeli

Üst kat planı (revak galerisi + 42 hücre)

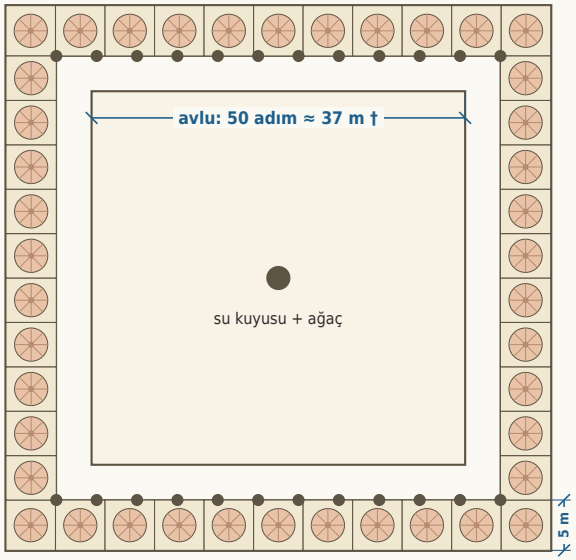


Divanyolu cephesi: geniş saçak altında sıra dükkânlar; giriş dehlizinden 21 basamaklı iki merdiven

Yaklaşık ölçek 1:750

0 20 m


Alt kat (ahır + mahzenler) – bir kanat

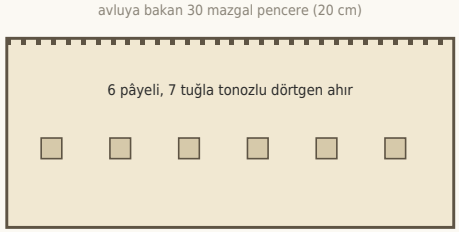

Yaklaşık ölçek 1:880

0 20 m

Tek hücre planı (16 × 16 ayak)

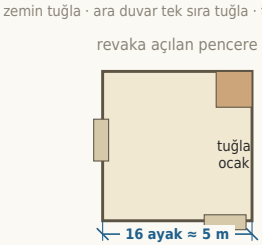

Yaklaşık ölçek 1:250

0 5 m

Ölçüler (Dernschwam)

Bina derinliği (sokak–avlu)	**31 adım ≈ 23 m**
Avlu	**50 × 50 adım ≈ 37 × 37 m †**
Revak her kenar	**48 adım (çevre 192)**
Revak örtüsü	**28 kurşun kaplı kubbe**
Üst kat hücre	**42**
Hücre boyutu	**16 × 16 ayak ≈ 5 × 5 m (bazı 12 ayak)**
Ahır	**6 pâye / 7 tuğla tonoz**
Mazgal pencere	**30 adet, 20 cm**
Giriş merdiveni	**2 × 21 basamak**

Hücre özellikleri

Tuğla döşeli zemin, tek sıra tuğla ara duvar, kubbeli tavan, küçük tuğla ocak; iki pencereden biri revaka (kepenksiz, camsız), diğeri dışarıya (taş söveli, demir parmaklıklı, tahta kepenkli) açılır.


Adım–metre dönüşümü bina derinliğinden türetilmiştir (1 adım ≈ 0,74 m) †. Hücre dağılımı (11+10+11+10) şematiktir.

Temsili şema. Boyutlar belgedeki verilerden alınmıştır; † işaretli değerler türetilmiş / oransal / kaynakta bulunmayan varsayımdır. Ölçek A4 yatay %100 yazdırmada geçerlidir.

Hanlar, Saraçhane ve Meslek Bölgeleri – Şemalar


Kürkçü Han · Balkapanı · Saraçhane · Sultanpazarı · Yedikule Debbağhaneleri

Saraçhane (4. Tepe) – 116 dükkân

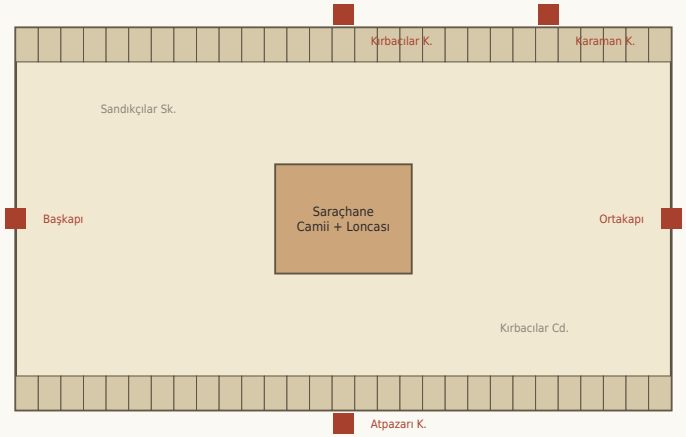

Ölçeksiz / şematik yerleşim

Sultanpazarı (Fatih Camii–Saraçhane arası)

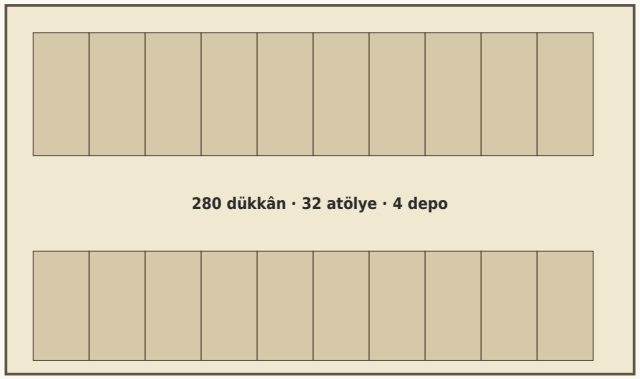

Fatih Külliyesi'nin güneyi · iç sokaklar ihtisas kollarına ayrılmış

Ölçeksiz / şematik yerleşim


Kürkçü Han (1467) – iki avlulu şema



iki katlı · 115 dükkân · Mahmud Paşa vakfı · kürkçü + derici merkezi

Ölçeksiz / şematik yerleşim

Yedikule (Kazlıçeşme) Debbağhaneleri ve diğer hanlar

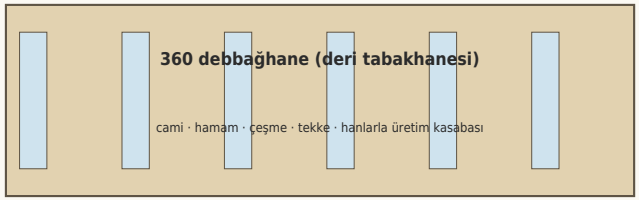

Balkapanı Hanı: altında L planlı sütunlu Bizans mahzeni
Kanuni devri: Büyük + Küçük Rüstem Paşa Hanları, Süleymaniye Hanı, Burmalı Han

İç kasa/avlu hücreleri 5–10 m² · sokağa açılan dükkânlar 10–20 m²

Ölçeksiz / şematik yerleşim

Sayısal veriler

Saraçhane (1475)	**116 dükkân · 5 kapı**
Sultanpazarı	**280 dükkân, 32 atölye, 4 depo**
Kürkçü Han (1467)	**115 dükkân · 2 avlu**
Debbağhane (Kazlıçeşme)	**360**
Han içi dükkân/mahzen	**5–10 m²**
Han dış dükkân	**10–20 m²**

Meslek mahalleleri

Bozahaneler (Eminönü), Debbâğîn/Dericiler (Unkapanı), Debbağ Yunus Mescidi ve Demirciler Mahallesi (Fatih).

Saraçhane kapıları: Başkapı, Ortakapı, Kırbacılar, Atpazarı, Karaman. Kâgir kemerli, kepenkli dükkânlar; iç sokaklar Sandıkçılar Sokağı ve Kırbacılar Caddesi gibi ihtisas kollarına ayrılır.


Tüm şemalar ölçeksizdir †; yalnız adet ve alan verileri belgeden alınmıştır.

Temsili şema. Boyutlar belgedeki verilerden alınmıştır; † işaretli değerler türetilmiş / oransal / kaynakta bulunmayan varsayımdır. Ölçek A4 yatay %100 yazdırmada geçerlidir.

16. Yüzyıl İstanbul Evi (Menzil) – Avlu Planı ve Kesit

Tek/iki katlı eklentili düzen · ortalama 2,57 oda · müstakil mutfak yalnız %6

Zemin kat planı (kuzey yukarı)

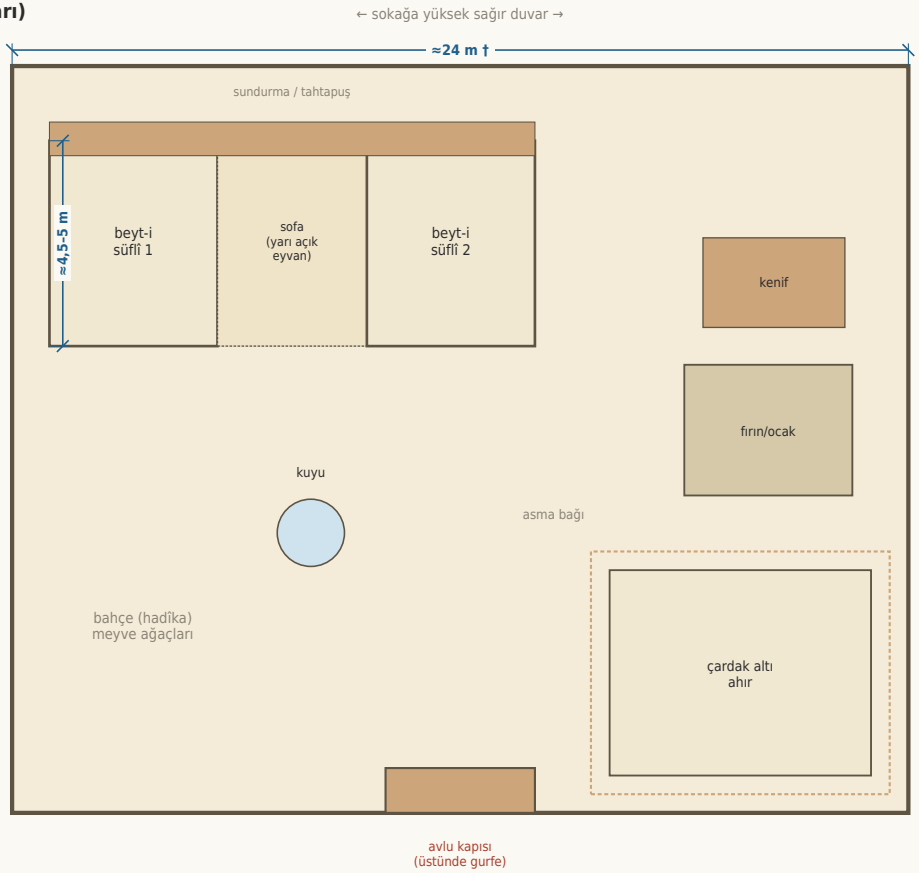

Yaklaşık ölçek 1:200

Kapı hattı kesiti: sağır sokak duvarı ve kapı üstü gurfe



Ölçeksiz / şematik yerleşim

İstatistik

Ev başına ortalama oda	**2,57 (17. yy başı 3,7)**
İki katlı / tek katlı / üç katlı (17. yy)	**%74,3 / %20 / %2,9**
Müstakil mutfak	**%6**
Selamlık–Haremlik ayrımı	**%12,5**
Çakıl ev / taş ev değeri	**~250 / ~300 akçe**

Kurallar

Tuvalet (kenif), mutfak/fırın, kuyu, kiler, ahır ve özel hamam daima zemin katta veya avluda; üst katta hiç örneği yoktur. Üst kat çoğunlukla kapı üstündeki tek gurfedir. Kapalı koridor (dehliz) 80 evlik örnekte yalnız 2 evde.

Sofa, 19. yy'daki gibi kapalı merkezî hol değil, iki oda arası yarı açık eyvan veya odaların önündeki sundurmadır. Çıkmalar ölçülü olmalıdır (Sinan'ın 1567 hükmü).


Örnek (İVTD 445): iki beyt-i süflî, ortası sofa, bir gurfe, bir ahır, bir kenif, bir bahçe. Avlu ve oda mesafeleri oransaldır †.

Renkler: toprak boya kırmızısı (dikme/söve), kahverengi, sarı, kireç fildişi beyazı.

Başoda – İç Mekân Planı ve Duvar Görünüşü

4,5 × 4,5 m örnek oda · 1:20 iç mekân maketi için

Plan (giriş altta)

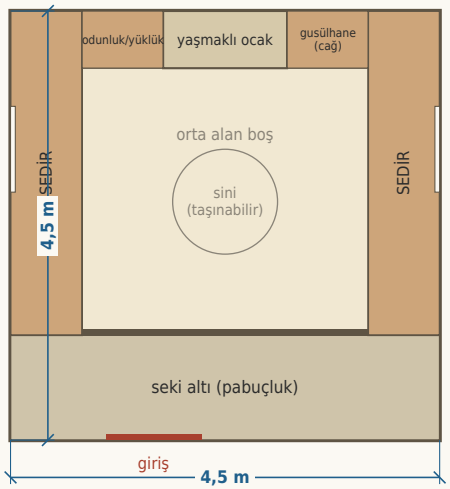

Yaklaşık ölçek 1:79

0 2 m

Ocak duvarı görünüşü (1:20)



Yaklaşık ölçek 1:84

0 2 m

Ölçüler

Oda planı	**~4–5 m kare**
Han hücreleri	**12–16 ayak**
Seki yüksekliği (saray)	**44 cm**
Sedir yüksekliği	**30–45 cm**
Gusülhane taş zemin	**~70 cm**
1:20 ölçekte 4,5 m	**22,5 cm**
1:20 ölçekte sedir	**~1,8 cm**

Donatı

Orta alan boş bırakılır; yemekte sini getirilir, geceleri yüklükten döşek serilir; zemin halı/kilim. Seki altında ayakkabı çıkarılır.

Sedir pencereli duvarlar boyunca 2–3 cephede L/U düzende minder ve yastıklarla; yaşmaklı ocak sağır duvarın ortasında; iki yanında yüklük dolabı, bir yanda odunluk, diğerinde kara taş gusülhane.

Alt pencereler demir parmaklıklı, tahta kepenkli, kafesli (mütevazı yapıda cam yok); üst revzenlerde dışta düz beyaz cam, içte alçı kayıtlı renkli cam.

Plandaki sedir/ocak/dolap genişlikleri oransaldır †.

Ölçek Stratejisi ve Çeviri Tablosu

Üç kademeli maket için hazır boyut hesapları

Gerçek ölçüden maket ölçüsüne (cm)

Yapı / öğe	Gerçek	1:2.000	1:500	1:200	1:20
Süleymaniye ana kubbe çapı	**27,45 m**	1,37 cm	5,49 cm	13,7 cm	137,2 cm
Süleymaniye harimi (kenar)	**69 m**	3,45 cm	13,8 cm	34,5 cm	345,0 cm
Süleymaniye dış avlu (216×144)	**216 m**	10,8 cm	43,2 cm	108,0 cm	1080,0 cm
Süleymaniye minaresi (76 m)	**76 m**	3,80 cm	15,2 cm	38,0 cm	380,0 cm
Mihrimah ana kubbe çapı	**20,25 m**	1,01 cm	4,05 cm	10,1 cm	101,2 cm
Mihrimah avlusu (57 m)	**57 m**	2,85 cm	11,4 cm	28,5 cm	285,0 cm
Yavuz Selim harimi (24,35)	**24,35 m**	1,22 cm	4,87 cm	12,2 cm	121,8 cm
II. Bayezid kubbe çapı	**16,78 m**	0,84 cm	3,36 cm	8,39 cm	83,9 cm
Haseki Hamamı uzunluğu	**75 m**	3,75 cm	15,0 cm	37,5 cm	375,0 cm
Arz Odası uzun kenar (24,05)	**24,05 m**	1,20 cm	4,81 cm	12,0 cm	120,2 cm
Arz Odası kısa kenar (18,70)	**18,7 m**	0,94 cm	3,74 cm	9,35 cm	93,5 cm
Has Oda Kasrı kenarı (23,5)	**23,5 m**	1,18 cm	4,70 cm	11,8 cm	117,5 cm
Bozdoğan Kemeri uzunluğu	**971 m**	48,5 cm	194,2 cm	485,5 cm	4855,0 cm
Eğrikapı Maksemi (8,25)	**8,25 m**	0,41 cm	1,65 cm	4,12 cm	41,2 cm
Başoda (4,5 m)	**4,5 m**	0,23 cm	0,90 cm	2,25 cm	22,5 cm
Sedir yüksekliği (0,40 m)	**0,4 m**	0,02 cm	0,08 cm	0,20 cm	2,00 cm

Önerilen üç kademeli ölçek

1) 1:2.000 – 1:2.500: Bütüncül Suriçi kentsel maketi (≈2,5 × 2,0 m tabla): yedi tepe, 3 kademeli kara surları + kuru hendek, Haliç/Marmara iskeleleri, 971 m Bozdoğan Kemeri, Eğrikapı Maksemi, Langa ve Çukurbostan bostanları, 13 nahiye / 219 Müslüman mahallesi + gayrimüslim mahalleleri, külliyeler.
2) 1:200 – 1:500: Topkapı Sarayı ve külliyeler detay maketi (dört avlu, 10 mutfak bölmesi, Kubbealtı, Dış Hazine, Arz Odası, Has Oda, Fatih Köşkü, Harem taşlıkları). Üst kubbeler çıkarılabilir (kesitli) yapılır.
3) 1:20 – 1:25: 16. yy İstanbul evi (menzil) ve çarşı dükkânı iç mekân maketi; 4,5 × 4,5 m Başoda 1:20'de 22,5 × 22,5 cm; iki duvarı açık kesit.

Dönem yanılgılarını önleme listesi (makette olmayacaklar)

- Sultanahmet Camii (1609–16) · Yeni Cami ve Mısır Çarşısı (17. yy) · Nuruosmaniye (1749–55) · Fatih Camii'nin 1771 yapısı · Kapalıçarşı sokak tonozları (1701 sonrası)
- Topkapı: Bağdat, Revan, Seferli, III. Ahmed Kütüphanesi, Mecidiye · Ayasofya'da 4 minare ve Sinan payandaları · 19. yy çok katlı orta sofalı konaklar
- Haseki Camii'nde 1612 ikinci kubbe · Süleymaniye dışında 17.–19. yy eklentileri (örn. Yavuz Selim şadırvan saçağı)